
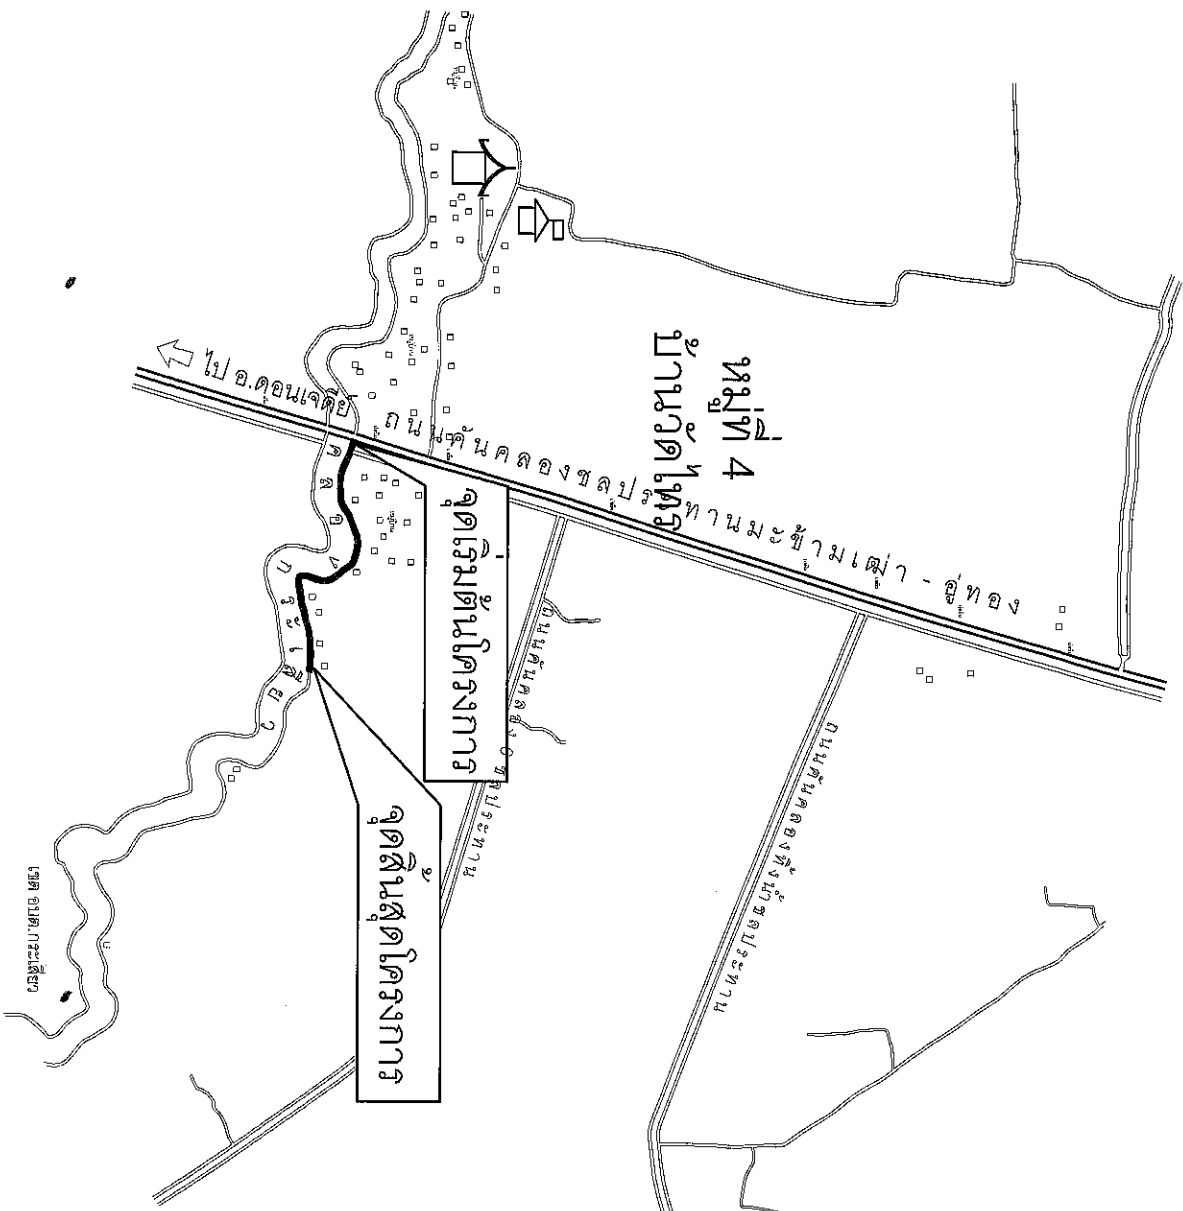


## โครงการก่อสร้างถนน ค.ศ.ล.หมู่ 4 บ้านวัดไทร

สถานที่ดำเนินการ เริ่มจากถนนลาดยางเดิมบริเวณสะพานข้ามคลองชลประทาน  
กม.24+394.60 ถึง บริเวณบ้านนางประหยัด แสงพันธ์ุ

ปริมาณงาน กว้าง 5.00 เมตร ยาว 300 เมตร หนา 0.15 เมตร ตามที่แบบกำหนด

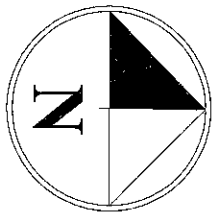

# แผนที่พอลีกาเพกติกโครงการ

|                                                |
|------------------------------------------------|
| กองช่าง                                        |
| องค์การบริหารส่วนตำบลหัวเขา                    |
| สำรวจ/เขียนแบบ                                 |
| นายเอี่ยม ศรีอริยะชัย<br>ผู้ช่วยนายก อบจ. ยะลา |
| สำรวจ/เขียนแบบ                                 |
| นางสาวสุภาวดี รอดทอง<br>นางสาวสุภาวดี รอดทอง   |
| ตรวจสอบ                                        |
| นายสุวิทย์ วัฒนวรรณ<br>นายสุวิทย์ วัฒนวรรณ     |
| อนุมัติ                                        |
| นายอภัย ทองรอด<br>นายก อบจ. ยะลา               |
| แบบโครงการ                                     |
| ก่อสร้างถนน ล. 1/11                            |
| แสดง                                           |
| - แผนที่พอลีกาเพกติก                           |
| จำนวนแผ่นที่ 1/11                              |

ข้อกำหนดเฉพาะงานและรายการประกอบแบบ

บทกำหนด ด้านวัสดุก่อสร้าง

1.วัสดุ กรวดทรายหรือดินและวัสดุคัดเลือกต่างๆ

1.1 ผู้รับจ้างต้องมีโรงงานชุดหรือลอก กรวด ทรายหรือดินในที่ดินกรรมสิทธิ์ หรือต้องมีเอกสารยินยอมให้ใช้ผลิตหินจากโรงงานชุดหรือลอก กรวด ทรายหรือดินในที่ดินกรรมสิทธิ์ที่ไม่ใช่ของผู้ยื่นเสนอ

1.2 ผู้รับจ้างต้องมีสำเนาใบอนุญาตประกอบกิจการโรงงาน(แบบ ร.ง.4) จากกรมโรงงานอุตสาหกรรมของผู้รับจ้างหรือผู้ให้ความยินยอมใช้ผลิตหินที่ขออนุญาตประกอบกิจการโรงงาน(แบบร.ง.4) จากกรมโรงงานอุตสาหกรรมต้องไม่หมดอายุ ถูกสั่งพักใช้ หรือเพิกถอน

1.3 กรณีไม่มีใบอนุญาตประกอบกิจการโรงงาน(แบบ ร.ง.4) จากกรมโรงงานอุตสาหกรรมให้ใช้หนังสือรับรองการตั้งหน่วยงานผลิตการชุดหรือลอก กรวด ทรายหรือดินในที่ดินกรรมสิทธิ์สำหรับหน่วยงานก่อสร้าง จากหน่วยงานอุตสาหกรรมแทน ของผู้รับจ้าง หรือผู้ให้ความยินยอมใช้ผลิตหินที่ ขอนหนังสือรับรองกล่าวต้องไม่หมดอายุ ถูกสั่งพักใช้หรือเพิกถอน

2. ปูนซีเมนต์และคอนกรีตผสมเสร็จ

2.1 ปูนซีเมนต์(สำหรับงานวางท่อ งานคอนกรีตโครงสร้างอื่นๆ)ที่ใช้ ต้องมีคุณสมบัติถูกต้องตามมาตรฐานผลิตภัณฑ์อุตสาหกรรมปูนซีเมนต์ปอร์ตแลนด์ มอก.15 ปูนซีเมนต์ที่ใช้ อาจบรรจุอยู่ในไซโล หรือเป็นแบบบรรจุถุงก็ได้ ถ้าเป็นแบบบรรจุถุง ผู้รับจ้างจะต้องจัดทำใบรับประกันซีเมนต์ที่เหมาะสม เพื่อป้องกันไม่ให้น้ำชื้นในซีเมนต์ขึ้น หัวนำปูนซีเมนต์ที่จับตัวเป็นก้อนปนอยู่มาใช้งาน ปูนซีเมนต์ที่ใช้ตลอดงานตามสัญญาต้องเป็นตราและประเภทเดียวกัน เว้นแต่จะได้รับความเห็นชอบจากคณะกรรมการตรวจรับพัสดุ และผู้ควบคุมงานเป็นอย่างไร

2.2 คอนกรีตที่จะนำมาใช้เพื่อจวางจร จะต้องเป็นคอนกรีตผสมเสร็จ ตาม มอก.213-2553 ซึ่งผลผลิตโดย โรงงานผลิตคอนกรีตผสมเสร็จ(Concrete Batching Plant) ที่ได้มาตรฐาน โดยต้องมีระยะทางจากสถานที่ผสมคอนกรีตผสมเสร็จถึงสถานที่ตั้งโครงการ ที่ต้องถ่ายเทคอนกรีตออกจากโถผสมภายในเวลา 1 ชั่วโมง 30 นาทีหลังจากเริ่มผสม ไม่น้อยกว่าให้ใช้คอนกรีตจากการผสมมือหรือโม่ผสมโดยตรง ขาด ทั้งนี้ให้ผู้รับจ้างแสดงเอกสารรับรองการใช้ผลิตภัณฑ์จากโรงงานผสม และ อัตราส่วนผสมคอนกรีต (Concrete Mix Design) ต่อผู้ว่าจ้างก่อนเข้าดำเนินการ เพื่อประกอบการพิจารณาแล้ว ของการใช้คอนกรีตผสมเสร็จที่ก่อสร้างทั้งหมดจากโรงงานผลิต เทียบปริมาณใกล้เคียง กับงานที่ก่อสร้าง(หรือมอบจ่ายสินค้าซึ่งระบุชื่อโครงการ,กำลังอัด,หมายเลขทะเบียนรถ,วันและเวลาที่ผลิต)

\*\*\*\*\* คอนกรีตที่นำมาใช้จะต้องเป็นคอนกรีตที่ผสมตามผลการออกแบบส่วนผสมคอนกรีตเท่านั้น ห้ามผู้รับจ้างเทคอนกรีตก่อนได้รับการอนุมัติผลการออกแบบส่วนผสมคอนกรีตหรืออื่นๆ ถ้าไม่โดยเด็ดขาด

|                                                 |
|-------------------------------------------------|
| กองช่าง                                         |
| องค์การบริหารส่วนตำบลห้วยขา                     |
| สำรวจ/เขียนแบบ                                  |
| นายอินทร์ ธรรมะธำ<br>ผู้ควบคุมช่างโยธา          |
| สำรวจ/เขียนแบบ                                  |
| นางศุภกานันท์ รอดทอง<br>นายช่างโยธาวินิจฉัยงาน  |
| ตรวจเช็ค                                        |
| นายตรีพิทย์ นาคสุวรรณ<br>นายช่างโยธาวินิจฉัยงาน |
| เห็นชอบ                                         |
| นางพ. เกษประทุม<br>ปลัดองค์การบริหารส่วนตำบล    |
| อนุมัติ                                         |
| นายสมนึก ทองรอด                                 |
| นายช่างโยธาวินิจฉัยงาน                          |
| แบบในโครงการ                                    |
| ก่อสร้างถนนค.ส.ท. 4 บ้านวัดไร่                  |
| แสดง                                            |
| มาตรฐานงานจราจรตามกฏกระทรวง                     |
| จำนวนแผ่นที่ 2/11                               |
| หมายเหตุ                                        |

บทกำหนด ด้านวัสดุก่อสร้าง(ต่อ)

### 3.1 วัตถุประสงค์ (วัตถุประสงค์ของรูป) เพื่อแสดงประเภทของวัสดุหรือคุณสมบัติของวัสดุที่จะใช้ในการก่อสร้างเป็นวัสดุที่ผลิตภายในประเทศ

3.2 ให้ผู้รับจ้างต้องใช้เวลาผลิตภายในประเทศ ไม่น้อยกว่าร้อยละ 90 ของปริมาณเหล็กที่ใช้ทั้งหมดตามสัญญา โดยก่อนส่งมอบงานให้แสดงรายการใช้เหล็กภายในประเทศ เสนอให้ประธานกรรมการตรวจรับวัสดุ ครวจสอบและพิจารณาว่า

4.1 วิเคราะห์งานที่ได้รับมอบหมายและจัดสรรทรัพยากรบุคคลให้เหมาะสมกับงาน

4.2 การเก็บและแข่งขันคอนกรีตจากสนาม และการทดสอบหาค่าความต้านทานแรงอัดในช่องปฏิบัติการทดลอง

คือนักปฏิวัติในสนาม

งานให้เพิ่มพ้อ คอนกรีตให้ทำการทดสอบหาค่าความยุบตัว(SLUMP) ทดลองหาค่าความยุบตัวและอย่างน้อยที่สุดต้องทำการทดสอบ 1 ครั้งต่อการผลิตคอนกรีต 50 ลูกบาศก์เมตร โดยทำการทดสอบเมื่อเริ่มเทคอนกรีตและทุกครั้งที่มีการหล่อแต่ละคอนกรีตตัวอย่าง หากไม่มีเครื่องมือทดสอบหรือไม่ได้กับตัวอย่างหรือทดสอบ (ผู้ควบคุมงานอาจพิจารณาทดสอบกับหน้างานจริงที่เทคอนกรีตแล้วผู้รับจ้างต้องรับผิดชอบค่าใช้จ่าย) โดยค่าความยุบตัว(SLUMP) ให้ใช้ 7.5 ซม. บวกลบ 2.5 ซม.

4.2.2 การเก็บตัวอย่างสำหรับทดสอบหาค่าความต้านแรงอัดของคอนกรีต ซึ่งทำให้การเทในแต่ละวันจะต้องเก็บไม่น้อยกว่าวันละ 1 ครั้ง หรือน้อยกว่า 1 ครั้งต่อการผลิตคอนกรีต 120 ลูกบาศก์เมตรหรือน้อยกว่า 1 ครั้งต่อคอนกรีตที่ใช้เทพื้น หรือหล่อผนังทุกพื้นที่ 450 ตารางเมตร หรือน้อยกว่า 1 ครั้งต่อคอนกรีตที่เทโครงสร้างแต่ละส่วน การหล่อและตั้งตัวอย่างคอนกรีต ผู้รับจ้างจะต้องดำเนินการเอง และบนแผงตัวอย่างทุกแห่งให้วางรายละเอียด วัน เดือน ปี ที่หล่อ ชื่อผู้รับจ้าง ชื่องานก่อสร้าง และส่วนของโครงสร้างให้ชัดเจน เช่น STA.กม.ที่เท่าไร โดยใช้วัสดุคุณสมบัติเช่นลงบนแผงคอนกรีต ขณะที่ยังไม่แข็งตัว และต้องรอรอบครบ 24 ชั่วโมง จึงถอดแบบและรับส่งให้ผู้ควบคุมงานโดยด่วน

|                                          |   |
|------------------------------------------|---|
| กองช่าง                                  |   |
| องค์การบริหารส่วนตำบลห้วยตอก             |   |
| สำรวจ/เขียนแบบ                           | นางอโยธิน ศรีอริยะ<br>ผู้เขียน/ช่างโยธา   |
| สำรวจ/เขียนแบบ                           | นางสาวศุภมาส รอดทอง<br>นางสาวโยธนา นามงาน   |
| ตรวจสอบ                                  | นายสุวิทย์ หุตสุวรรณ<br>นายช่างโยธานำงาน   |
| เห็นชอบ                                  | นาง นพ เกษประทุม<br>ช่าง   |
| อนุมัติ                                  | นายกองค์การบริหารส่วนตำบลห้วยตอก   |
| นายอเนก นามงาน                           |   |
| แบบโครงการ                               | ทำเสร็จหมด, ส. ๓, ๔, ๕, ๑๐๐ |
| แปลน                                     |   |
| - ชื่อที่ทางเทศบาล<br>และราชการประกอบแบบ |   |
| จำนวนแผ่นที่                             | 3/11   |
| หมายเลข                                  |   |

# ข้อกำหนดเฉพาะงานและรายการประกอบแบบ

## ขอบข่ายของสัญญาจ้าง

1. เมื่อองค์การบริหารส่วนตำบลหัวเขา ได้ส่งมอบพื้นที่ให้ผู้รับจ้างแล้ว ผู้รับจ้างจะต้องดำเนินการก่อสร้างให้แล้วเสร็จตามสัญญาที่กำหนดไว้ ส่วนพื้นที่ใดที่มีปัญหาและอุปสรรค องค์การบริหารส่วนตำบลหัวเขา ขอสงวนสิทธิ์ในการตัด - เพิ่ม - ลดเนื้องาน หรือแก้ไขสัญญาได้
2. งานก่อสร้างตามสัญญาจ้างต้องเป็นไปตามรูปแบบ และรายการก่อสร้าง ซึ่งผู้จ้างและผู้รับจ้างได้ลงลายมือชื่อในฐานะคู่สัญญาและยอมรับเป็นส่วนหนึ่งของสัญญาจ้าง
3. ผู้รับจ้างรับว่าได้ตรวจสอบสถานที่ก่อสร้าง รายละเอียดตลสัญญา ข้อกำหนดพิเศษต่างๆ รวมทั้งรูปแบบและรายการก่อสร้างทุกฉบับโดยตลอด และเข้าใจความหมายโดยแจ้งชัดแล้ว จะแสดงการรับรู้สภาพใดๆ อันเกี่ยวเนื่องกับการปฏิบัติงานตามสัญญานี้ไม่ได้
4. หากมีงานส่วนหนึ่งส่วนใดที่ปรากฏในแบบ แต่จำเป็นต้องเพิ่มเติมให้งานบรรลุตามวัตถุประสงค์และถูกต้องตามหลักวิชาช่างที่ดี ให้ผู้รับจ้างดำเนินการในส่วนนั้น ตามคำแนะนำของผู้ออกแบบและผู้ควบคุมงาน โดยเคร่งครัดเพื่อให้งานบรรลุตามวัตถุประสงค์โดยไม่ได้เป็นงานเพิ่ม และเอาเงินเพิ่มอีกแต่อย่างใด
5. กรณีรูปแบบบกพร่องหรือขัดแย้งกับรายการให้ถือเอาการปฏิบัติงานที่ดีกว่า โดยถือเอาคำตัดสินของผู้จ้างเป็นอันสิ้นสุด และผู้รับจ้างจะต้องยอมทำงานนี้ให้เสร็จเรียบร้อยโดยไม่คิดเอาเงินเพิ่มแต่อย่างใด
6. สิ่งที่ไม่ได้กล่าวไว้ในรูปแบบหรือรายการแต่เป็นส่วนจำเป็นต่อการทำงาน เพื่อให้งานสำเร็จสมบูรณ์โดยรวดเร็วที่ดี และถูกต้องตามหลักวิชาช่าง ให้ถือเป็นส่วนที่ผู้รับจ้างต้องดำเนินการด้วย โดยผู้รับจ้างจะต้องยอมทำงานนี้ให้โดยไม่ได้คิดเอาเงินเพิ่มอีกแต่อย่างใด
7. ผู้รับจ้างจะต้องเข้าใจปัญหาต่างๆ และรู้ถึงสภาพแวดล้อมของจริงที่มีอยู่เดิม ในบริเวณของสถานที่ก่อสร้างและบริเวณข้างเคียง ตลอดจนต้องรับผิดชอบในการแก้ไข เคลื่อนย้าย หรือรื้อถอนให้ถูกต้องตามสภาพพื้นที่ที่แท้จริง จนสามารถเข้าไปดำเนินการปรับปรุงตามรูปแบบและรายการได้ตามวัตถุประสงค์
8. รูปแบบ และรายการที่กำหนดให้ไว้เป็นเพียงแนวทางการปฏิบัติงานอาจเปลี่ยนแปลงตามความเหมาะสมและสอดคล้องกับสภาพที่จริง โดยได้ประโยชน์ใช้สอยเต็มที่ ซึ่งการออกแบบที่สร้างขึ้นจะต้องมีปริมาณเท่ากับหรือมากกว่ารูปแบบรายการเดิม โดยผู้จ้างเป็นผู้ให้ความเห็นชอบ และถือเป็นกรับเปลี่ยนแบบหรือเพิ่มเนื้องานตามรายการในสัญญาแต่อย่างใด
9. ระยะต่าง ๆ ที่กำหนดไว้ในแบบหรือแผนผัง หากไม่สามารถดำเนินการได้ตามสภาพความเป็นจริงให้อยู่ในดุลยพินิจของผู้ควบคุมงานและคณะกรรมการตรวจสอบพื้นที่ในการที่จะแก้ไข และเปลี่ยนแปลงได้ตามความเหมาะสม
10. เนื้องานที่กำหนดไว้หากมีเหลือเกินจากแผนที่ส่งขงที่กำหนดไว้ยินยอมให้ก่อสร้างเข้าเป็นทางร่วมทางแยกในถนนซอยบริเวณใกล้เคียงได้ โดยให้อยู่ในดุลยพินิจของผู้ควบคุมงานและคณะกรรมการตรวจสอบพื้นที่

|                                   |                                                   |
|-----------------------------------|---------------------------------------------------|
| กองช่าง                           |                                                   |
| องค์การบริหารส่วนตำบลหัวเขา       |                                                   |
| ผู้ตรวจ/เขียนแบบ                  | นายโยธิน ศรีอริยะธา<br>ผู้ควบคุมงานต่างอำเภอ      |
| ผู้ตรวจ/เขียนแบบ                  | นางสาวศุภมาส รอดทอง<br>นางอัสมาฮ์ อาลี            |
| ตรวจสอบ                           | นายศิริทิพย์ พูลศิริธรรม<br>นายศุภางค์ ยอฮันดี    |
| เห็นชอบ                           | นายก อบจ. ประทุม<br>ปลัดองค์การบริหารส่วนตำบล     |
| อนุมัติ                           | นายธนู พงษ์รอด<br>นายกองค์การบริหารส่วนตำบลหัวเขา |
| งบ/โครงการ                        |                                                   |
| ก่อสร้างขนาด ๔.๕ ไร่ ๔ บ้านวัดไทร |                                                   |
| แสดง                              | - ชื่อทางเขต<br>และรายการประกอบแบบ                |
| จำนวนแผ่นที่                      | 4/11                                              |
| หมายเหตุ                          |                                                   |

ข้อกำหนดเฉพาะงานและรายการประกอบแบบ

ขอบข่ายของสัญญาจ้าง (ต่อ)

- 1. ระยะเวลาที่กำหนดในฝั่งหากตลาดเคลื่อนไปจากสภาพจริง ให้ถือสภาพจริงเป็นเกณฑ์
- 12. ในการก่อสร้าง หากผู้รับจ้างดำเนินการครบตามรูปแบบแล้ว ยังมีปริมาณงานที่ต้องดำเนินการอีก ให้ผู้รับจ้างดำเนินการในบริเวณเดียวกันและ/หรือ บริเวณต่อเนื่อง ทั้งนี้การดำเนินการดังกล่าว จะต้องก่อให้เกิดประโยชน์แก่ประชาชนและองค์การบริหารส่วนตำบลหากมากที่สุด โดยผู้ควบคุมงานจะเป็นผู้กำหนดให้ระยะระหว่างการก่อสร้าง และเมื่อว่าเป็นการดำเนินการผิดรูปแบบและรายการแต่อย่างใด รวมถึงไม่ถือเป็นการเปลี่ยนแปลงแก้ไขสัญญาจ้าง

หน้าที่และความรับผิดชอบของผู้สัญญา

1. ให้ผู้รับจ้างจัดทำ/จัดส่งแผนงานก่อสร้าง เพื่อใช้เป็นการติดตามและควบคุมงานของพนักงานก้าวหน้า การทำงานให้แล้วเสร็จตามวัตถุประสงค์ของโครงการและระยะเวลาที่สัญญาจ้างกำหนด

- 2. ผู้รับจ้างจะต้องปฏิบัติตามหลักหรือคำแนะนำการด้วยวิธีอื่นๆใด เพื่อแสดงตำแหน่งของงานทุกช่วง ระยะหากเกินไม่เกิน 50 เมตร นับจากจุดเริ่มต้นไปจนถึงจุดสิ้นสุดความยาวที่จะทำการก่อสร้าง และจะต้องรักษาวัว จนกว่าผู้จ้างได้รับมอบงานตามสัญญาจ้างที่ได้แล้วเสร็จ ลงหมดแนว หมดระดับและหมดหลักอื่นๆใด ซึ่งจะต้องทำให้เพิ่มเติมเพื่อประโยชน์ในการก่อสร้าง ผู้รับจ้างจะต้องเป็นผู้จัดทำและรับ
- 3. ให้ผู้รับจ้างจัดทำป้ายประกาศต่างๆ มีข้อความประกาศ และมีจำนวนตามที่คุณงานกำหนด ติดตั้งไว้ ณ บริเวณสถานที่ก่อสร้าง และจะต้องดูแลรักษาไม่ให้เกิดการเสียหาย หรือเกิดการลบเลือนของข้อความที่ประกาศตลอดระยะเวลาการก่อสร้าง
- 4. ผู้รับจ้างจะต้องรับผิดชอบแต่ฝ่ายเดียวต่อการชำรุดเสียหายที่เกิดขึ้นเกี่ยวกับสิ่งสาธารณูปโภคทั้งปวงรวมทั้งทรัพย์สินอื่น ทั้งที่เป็นของทางราชการ และของเอกชนที่เกิดจากการกระทำของผู้รับจ้าง ไม่ว่าจะโดยจงใจหรือโดยประมาทเลินเล่อก็ตาม

ในการณที่ที่เกิดการชำรุดเสียหายแก่สิ่งดังกล่าวในวรรคก่อน ผู้รับจ้างจะต้องชดใช้เงิน หรือต้องทำการบูรณะซ่อมแซมหรือทำขึ้นใหม่ ให้กลับคืนสภาพเดิมโดยเร็ว หากผู้รับจ้างเพิกเฉย หรือบิดพลิ้วดำเนินการหรือผู้จ้างเห็นว่าผู้รับจ้างกระทำการล่าช้า ผู้จ้างจะเข้าดำเนินการดังกล่าวแทนโดยผู้รับจ้างจะต้องออกเงินค่าใช้จ่ายในการนี้ทั้งหมด หรือผู้จ้างอาจบอกเลิกสัญญาจ้างเสียก็ได้ พร้อมขมขมิสิทธิเรียกร้องค่าเสียหายอื่นๆด้วย

5. สัญสาราณูปโภคต่างๆที่ติดขวางการก่อสร้าง และมีความจำเป็นต้องเคลื่อนย้ายให้พ้นออกไป ให้ผู้รับจ้างรับแจ้งผู้ว่าจ้างทราบเป็นลายลักษณ์อักษร เพื่อให้ผู้จ้างจะได้พิจารณาช่วยเหลือติดข้อความร่วมเมื่อจากหน่วยงานที่เกี่ยวข้องจัดการย้ายให้

6. ผู้รับจ้างสัญญาว่า โรงงานชั่วคราวหรือวัสดุก่อสร้างหรือการจราจรรถยนต์ ผู้รับจ้างจะไม่ทำให้ติดขวางการสัญจรของประชาชนและยานพาหนะที่ผ่านเข้ามา และเมื่อเลิกงานแล้ว ผู้รับจ้างจะต้องเก็บเครื่องมือเครื่องใช้ เครื่องขุ่นแรง ยานพาหนะ อุปกรณ์การก่อสร้างไว้ภายในบริเวณที่กำหนดเท่านั้น

7. การก่อสร้างโครงสร้างคอนกรีต เช่น งานก่อสร้าง ถนน รางวี บ่อพัก ท่อระบายน้ำ รางระบายน้ำ ดาดคู ดาดหน้าท่าระบายน้ำ เป็นต้น ให้ถือวันแล้วเสร็จสมบูรณ์ เมื่อได้มีการบ่มคอนกรีต ครบ 7 วัน นับตั้งแต่วันงานเสร็จเรียบร้อยแล้ว(กรณีไม่ต้องรอผลทดสอบ)

|                                                 |
|-------------------------------------------------|
| กองช่าง                                         |
| องค์การบริหารส่วนตำบลห้วยขา                     |
| คำรวจ/เขียนแบบ                                  |
| นายอินัน ศรีอรรถะอ้า<br>ผู้ช่วยนายช่างโยธา      |
| คำรวจ/เขียนแบบ                                  |
| นางสาวศุภกมล รอดทอง<br>นายช่างโยธาชำนาญงาน      |
| ตรวจ/เซ็น                                       |
| นายอัครวิทย์ คุ้มสุวรรณ์<br>นายช่างโยธาชำนาญงาน |
| เห็นชอบ                                         |
| นายก อบจ.น่าน                                   |
| นายอัครวิทย์ คุ้มสุวรรณ์<br>นายช่างโยธาชำนาญงาน |
| อนุมัติ                                         |
| นายก อบจ.น่าน                                   |
| นายอัครวิทย์ คุ้มสุวรรณ์<br>นายช่างโยธาชำนาญงาน |
| แบบ/วิศวกร                                      |
| นางสาวณนทาสี หนู 4 มีนาคม 2561                  |
| ได้ตั้ง                                         |
| - ผู้ออกแบบผลงาน<br>และรายการประกอบแบบ          |
| จำนวนแผ่นที่ 5/11                               |
| หมายเหตุ                                        |

# ข้อกำหนดเฉพาะงานและรายการประกอบแบบ

## หน้าที่และความรับผิดชอบของผู้สัญญา (ต่อ)

8. ผู้รับจ้างจะต้องไม่เอางานทั้งหมดหรือบางส่วนแห่งสัญญาไปจ้างช่วงอีกต่อหนึ่ง โดยไม่ได้รับความยินยอมเป็นลายลักษณ์อักษรจากผู้ว่าจ้างก่อน ทั้งนี้ นอกจากในกรณีที่สัญญาจะระบุไว้เป็นอย่างอื่น ความยินยอมดังกล่าวนี้ไม่เป็นเหตุให้ผู้รับจ้างหลุดพ้นจากความรับผิดชอบ หรือพ้นหน้าที่ตามสัญญา และผู้รับจ้างจะยังคงต้อง รับผิดชอบในความผิด และค่าเสียหายของผู้รับจ้างช่วง หรือของตัวแทน หรือของลูกจ้างของผู้รับจ้างช่วงนั้น ทบทวนประการ

9. งานบกพร่องใดๆ ไม่ว่าจะเกิดจากฝีมือไม่ดี ใช้วัสดุที่ด้อยคุณภาพ ความเสียหายจากความไม่ระมัดระวังหรือเหตุอื่นใดที่พบว่ามิใช่ก่อนการสิ้นสุดการประกันตามระยะเวลาในสัญญา ให้ผู้รับจ้างต้องชดเชยและให้ทำใหม่ โดยการทำและวัสดุที่ใช้ให้เป็นไปตามข้อกำหนด และการก่อสร้าง หรืออาจแก้ไขโดยวิธีอื่นใดในลักษณะที่ผู้ควบคุมงานและคณะกรรมการตรวจสอบและอนุญาตให้ทำได้ ข้อกำหนดดังกล่าวนี้ให้มีผลบังคับอย่างสมบูรณ์ โดยไม่ต้องคำนึงถึงว่างานบกพร่องดังกล่าวข้างต้นนั้นได้ทำโดยที่ผู้ควบคุมงานได้รู้แล้ว และในกรณีที่ถือข้อบกพร่องขึ้น เนื่องจากความบกพร่องของผู้รับจ้าง นอกจากผู้รับจ้างจะต้องเป็นผู้รับผิดชอบโดยสิ้นเชิงแต่ฝ่ายเดียว ในบรรดาความเสียหายที่เกิดขึ้นแล้ว ผู้ว่าจ้างอาจถือเป็นสาเหตุในการบอกเลิกสัญญาได้

10. วัสดุที่ใช้ในการก่อสร้างอยู่ในสภาพดีและใช้งานได้ ผู้รับจ้างต้องชดเชยวัสดุเหล่านั้นไปเก็บไว้ ณ สถานที่ ที่เจ้าหน้าที่ผู้ควบคุมงาน กำหนดให้ โดยไม่สามารถคิดค่าใช้จ่ายใดๆ จากผู้ว่าจ้างได้ทั้งสิ้น

11. เมื่อสิ้นสุดการปฏิบัติงานในแต่ละวัน ให้ผู้รับจ้างทำความสะอาดพื้นที่ก่อสร้างตลอดจนพื้นที่เกี่ยวเนื่องให้อยู่ในสภาพสะอาดเรียบร้อย ปราศจากเศษวัสดุ หรือสิ่งปฏิกูลอื่นใด ที่อาจก่อให้เกิดข้อพิพาทหรือเป็นเหตุแห่งความเดือดร้อนรำคาญของประชาชนในพื้นที่และผู้ใช้เส้นทางสัญจร

12. ให้ผู้รับจ้างจัดเตรียมสภาพถ่ายสี แสดงขั้นตอนการดำเนินงานของผู้รับจ้าง ประกอบไปด้วย ภาพถ่ายก่อนดำเนินการ ขณะดำเนินการทุกขั้นตอนตามรายการสัญญาและมาตรฐานการก่อสร้าง และ หลังดำเนินการแล้วเสร็จสมบูรณ์ เพื่อเป็นเอกสารประกอบการส่งมอบงานจ้าง

13. ผู้รับจ้างต้องรับผิดชอบในการอำนวยความสะดวกและปลอดภัยแก่ประชาชนผู้ใช้ทางโดยเฉพาะในบริเวณพื้นที่และเส้นทางที่ได้รับมอบจากผู้ว่าจ้างไปดำเนินการแล้วตลอดเวลา โดยการจัดทำ จัดหา และติดตั้งสิ่งจำเป็นต่างๆ เกี่ยวกับการจราจร จะเป็นค่าใช้จ่ายของผู้รับจ้าง และในขณะทำงานผู้รับจ้างต้องบำรุงรักษาเส้นทางให้ใช้สัญจรได้สะดวกและปลอดภัยตลอดเวลาก่อนการก่อสร้างเป็นอุปสรรคต่อการสัญจรอาจเปิดให้รถเดินทางเดียวได้โดยผู้รับจ้างจะต้องจัดหาติดตั้ง อุปกรณ์ และเครื่องหมายสัญญาณจราจร เตือนล่วงหน้าและป้องกันอุบัติเหตุ หากการสัญจรไม่สามารถมองเห็นในทิศทางตรงกันข้าม ผู้รับจ้างต้องให้พนักงานให้สัญญาณและจัดจราจรจราจรให้ผ่านได้โดยสะดวกหากมีความจำเป็นต้องปิดหรือปิดการจราจรเป็นบางช่วงจะต้องได้รับอนุญาตจากผู้ควบคุมงานก่อนและผู้รับจ้างจะต้องจัดทำทางเบี่ยงหรือสะพานเบี่ยงให้การจราจรผ่านได้ตามปกติก่อนที่จะทำการปิดทางเพื่อทำการก่อสร้าง พร้อมทั้งมีการแนะนำและเตือนผู้ใช้เส้นทางเป็นการล่วงหน้า โดยผู้รับจ้างต้องดูแลและบำรุงรักษาทางเบี่ยง หรือสะพานเบี่ยงให้อยู่ในสภาพที่ใช้งานได้ดี และสะดวกปลอดภัยตลอดเวลาที่ใช้งาน

|                                                      |
|------------------------------------------------------|
| กองช่าง                                              |
| องค์การบริหารส่วนตำบลหัวเขา                          |
| สำรวจ/เขียนแบบ                                       |
| นายสมิณ ศรีธรรมชา<br>ผู้ช่วยนายช่างโยธา              |
| สำรวจ/เขียนแบบ                                       |
| นางสาวศุภณัฐ รอดทอง<br>นายช่างโยธาวินิจฉัยงาน        |
| ตรวจ/เซ็น                                            |
| นายสุวิทย์ นุตสุวรรณ<br>นายช่างโยธาชำนาญงาน          |
| อนุมัติ                                              |
| นางนพ เกษมประทุม<br>ปลัดองค์การบริหารส่วนตำบลหัวเขา  |
| นายสมิณ ศรีธรรมชา<br>นายกองค์การบริหารส่วนตำบลหัวเขา |
| แบบ/โครงการ                                          |
| ก่อสร้างถนนค.ส.ล. หมู่ 4 บ้านวัดโพธิ์                |
| แสดง                                                 |
| - ชื่อภาพเฉพาะงาน<br>และรายการประกอบแบบ              |
| จำนวนแผ่นที่ 6/11                                    |
| หมายเหตุ                                             |

ข้อกำหนดเฉพาะงานและรายการประกอบแบบ

หน้าที่และความรับผิดชอบของผู้สัญญา (ต่อ)

14. การติดตั้งป้ายและสัญญาณความถี่ในการจราจรในขณะทำงาน ผู้รับจ้างต้องจัดให้มีป้ายและสัญญาณจราจร เพื่อเตือนและแนะนำผู้ใช้ทางทราบล่วงหน้า ให้ผู้ใช้ยานพาหนะด้วยความระมัดระวังมิให้เกิดอุบัติเหตุอันเนื่องมาจากการก่อสร้างกรณีที่เป็นต้องปิดกั้นทางที่ใช้สัญจรตามปกติต้องจัดให้มีแสงกั้นพร้อมป้าย หรือเครื่องหมายเตือนล่วงหน้า และในเวลากลางคืนต้องจัดให้มีแสงสว่างติดตั้งไว้ที่แสงกั้นด้วยในบริเวณที่กำลังก่อสร้าง การกองวัสดุไว้บนคันทาง ต้องจัดให้มีป้ายเตือนเพิ่มเติมเป็นกรณีพิเศษตลอดเวลากว่างาน และถ้าเป็นงานที่ทางบริเวณทางตัดหรือทางแยก นอกจากจะต้องติดตั้งป้ายเตือนบริเวณก่อสร้างแล้วยังต้องติดตั้งบนทางตัดหรือทางแยกสายที่มีจราจรจราจรผ่านบริเวณที่มีการก่อสร้างด้วยป้ายเครื่องหมายและสัญญาณจราจรรวมทั้งการติดตั้ง จะต้องเป็นไปตามแบบมาตรฐาน และหากจำเป็นจะต้องจัดให้มีแสงสว่างสามารถเห็นลักษณะและรายละเอียดของป้ายเครื่องหมายได้ชัดเจน

การควบคุมคุณภาพ การก่อสร้าง

1. การก่อสร้างหรือสิ่งที่จะต้องดำเนินการนอกเหนือจากที่กำหนดในแบบฉบับนี้ **ผู้สัญญา** ให้เป็นไปตาม มาตรฐานงานทางของ องค์การ

บริหารส่วนตำบลหัวเขา พ.ศ.2566 (ถ้ามี)

2. คอนกรีตที่จะเท ต้องเทติดต่อกันโดยสม่ำเสมอให้เต็มแต่ละช่วง และมีความหนาที่จะแบ่งได้ตั้งแต่ 1 เมตรขึ้นไปทุกครั้ง ห้ามหยุดเทคอนกรีตในแต่ละช่วงเป็นอันขาด หากมีเหตุขัดข้องใดๆ อันทำให้การเทคอนกรีตในแต่ละช่วงที่หยุดชะงักนานกว่า 30 นาที จะต้องรีบคอนกรีตที่แห้งแล้วในช่วงนั้นออกทิ้งเสียทั้งหมด หรือรีบทำรอยต่อเนื่องจากการก่อสร้าง(Construction Joint) ที่จุดนั้นทันที แต่ถ้าเหตุขัดข้องนั้น หยุดชะงักนานไม่เกินกว่า ระยะเวลาที่กำหนด ตรงแนวคอนกรีตที่แห้งแล้วกับที่จะเทใหม่ ให้ใช้ปลั๊ก คอนกรีตเก่าและใหม่ผสมกัน

3. การวางเหล็กเสริม เหล็ก Dowels และ Tie Bars จะต้องมีขนาดและอยู่ในตำแหน่ง ที่ถูกต้องตามที่กำหนดไว้ในแบบแปลนทุกประการ ในการฉีกลงและกรงเหล็กเสริม จะต้องแน่ใจว่าจะไม่เกิดการทรุดตัวในขณะเทคอนกรีต เมื่อผูกเหล็กต่างๆ เสร็จเรียบร้อยแล้ว ก่อนดำเนินการเทคอนกรีต ผู้รับจ้างต้องแจ้งให้ผู้ควบคุมงานตรวจสอบความเรียบร้อยของการผูกเหล็กและอื่นๆก่อน

4. ก่อนดำเนินการเทคอนกรีตครั้งแรกให้ผู้รับจ้างแจ้งเจ้าหน้าที่ผู้ควบคุมงานทราบล่วงหน้าในวันและเวลาราชการ อย่างน้อย 1-3 วัน เพื่อที่จะได้ประสานผู้ที่เกี่ยวข้อง เข้าทำการตรวจสอบ มาตรฐานของเครื่องมือในการผสมคอนกรีต ระยะเวลาในการขนส่งคอนกรีตจากแหล่งผลิตคอนกรีต ถึงสถานที่ก่อสร้าง และมาตรฐานการควบคุมการปล่อยขยะของกระบวนการจราจร

5. ก่อนทำการเทคอนกรีตทุกครั้งให้ผู้รับจ้างแจ้งผู้ควบคุมงานล่วงหน้าอย่างน้อย 1 วัน เพื่อตรวจสอบ ระดับ จำนวน และขนาดของเหล็กเสริมคอนกรีตให้เป็นไปตามรูปแบบและรายการที่สัญญาจ้างกำหนดเสียก่อน หากผู้รับจ้างดำเนินการไปโดยพลการ เจ้าหน้าที่ผู้ควบคุมงาน มีสิทธิสั่งให้หรือ สั่งแก้ไขใหม่ โดยผู้รับจ้างจะต้องยินยอมดำเนินการตาม โดยค่าวัสดุและค่าใช้จ่ายต่างๆ

จากการรับรองและแก้ไขใหม่ทั้งหมดที่เกิดขึ้น ให้เป็นภาระของผู้รับจ้างทั้งสิ้น และจะเรียกหรือค่าใช้จ่ายและระยะเวลาที่เพิ่มขึ้นจากผู้ว่าจ้างอีกมิได้

|                                                 |                                                                                       |
|-------------------------------------------------|---------------------------------------------------------------------------------------|
| กองช่าง                                         |                                                                                       |
| องค์การบริหารส่วนตำบลหัวเขา                     |                                                                                       |
| สำรวจ/เขียนแบบ                                  |  |
| นายไฉน ศรีอริยะชา<br>ผู้ช่วยช่างโยธา            |                                                                                       |
| สำรวจ/เขียนแบบ                                  |  |
| นางสาวกัญญา รอดทอง<br>นายช่างโยธาชำนาญงาน       |                                                                                       |
| ตรวจ                                            |   |
| นายสุวิทย์ ทุ่งสุวรรณ<br>นายช่างโยธาชำนาญงาน    |                                                                                       |
| เห็นชอบ                                         |    |
| จาก                                             |                                                                                       |
| นายพิ ภาณุประเสริฐ<br>ปลัดองค์การบริหารส่วนตำบล |                                                                                       |
| อนุมัติ                                         |    |
| นายณัฐ ทองรอด                                   |                                                                                       |
| นายกองค์การบริหารส่วนตำบลหัวเขา                 |                                                                                       |
| แบบโครงสร้าง                                    |                                                                                       |
| ก่อสร้างเขต ส.ล. หมู่ 1 บ้านวัดไทร              |                                                                                       |
| แสดง                                            |                                                                                       |
| -ชื่อทางหลวงชนบท<br>และรายการประกอบแบบ          |                                                                                       |
| จำนวนแผ่นที่ 7/11                               |                                                                                       |
| หมายเหตุ                                        |                                                                                       |



กรมการทะเบียนการค้าและภาษีศุลกากร

การควบคุมคุณภาพ การก่อสร้าง (๔๐)

6. งานรูปแบบ เมื่อประกอบแล้วต้องมั่นคงแข็งแรง และเมื่อถอดแบบออกแล้ว คอนกรีตจะต้องไม่เป็นโพรงหรืออื่นๆที่ไม่เรียบร้อย หรือรอยต่อเชื่อมใดๆจะต้องดำเนินการฉาบแต่งให้อยู่ในสภาพเรียบร้อย และไม่อนุญาตให้ใช้งานชุดดิน ผังดินเดิม ทดแทนแบบก่อสร้าง โดยเด็ดขาด

7. หลังจากเทคอนกรีตแล้ว ผู้รับจ้างจะต้องมีการดูแลป้องกันผิวทางคอนกรีตที่เทเสร็จแล้วไม่ให้กระแทกหรือฉีกขาด บรุษทุกที่จะเป็นเหตุทำให้ชำรุดเสียหาย จนถึงระยะเวลาไม่น้อยกว่า 28 วัน นับจากวันที่เทคอนกรีต และผู้รับจ้างจะต้องมีการบ่ม คอนกรีตจนกว่าจะได้ระยะเวลาครบไม่น้อยกว่า 28 วัน กรณีหยุดเทคอนกรีตในแต่ละครั้ง ให้หยุดเป็นแนวตั้งฉากพร้อมใส่หลักตามแบบ ขยายรอยต่อเพื่อการขยายหรือหดตัว (EXPANSION JOINT) โดยอนุโลม

๘. หากขณะก่อตัวขึ้นเกิดปัญหาและอุปสรรคให้แจ้งหรือประสานงานเจ้าหน้าที่ชุด และแหล่งส่งทางสื่อแจ้งปัญหาเพื่อพิจารณาต่อไป

9. ในกรณีแบบก่อสร้างไม่ชัดเจน ชัดแย้งกัน หรือไม่ตรงกับรายการก่อสร้าง ให้แจ้งผู้ควบคุมงานของผู้ว่าจ้าง และคณะกรรมการตรวจรับพัสดุ เพื่อพิจารณาแจ้งการแก้ไข อย่างหนึ่งอย่างใดเสียก่อนที่จะปฏิบัติงาน ถ้าผู้รับจ้าง ไม่ปฏิบัติตามนี้ หากมีข้อผิดพลาดใด ๆ ขึ้น ผู้รับจ้างต้องรับผิดชอบในข้อผิดพลาดนั้นๆ ให้ถูกต้องตามคำสั่งและรายการก่อสร้างทั้งหมด หรือขอต่ออายุสัญญาจ้างไม่ได้

การแก้ไขหรือแตกต่างที่เกิดขึ้นของผิวจราจรคอนกรีตเสริมเหล็ก

1. ผู้จรรจาจรรจนกฐินเตรียมเหล็ก เมื่อดำเนิการก่อสร้างแล้วเสร็จ จะต้องอยู่ในสภาพสมบูรณ์ เหมือนใหม่ ที่ไม่เคยผ่านการใช้งานมาก่อน ในการนี้ปรากฏว่ายแตกร้าว เนื่องจากการเปลี่ยนแปลงอุณหภูมิ หรืออื่นๆที่ไม่เกิดจากอันตรายส่วนผสมหรือวิธีการก่อสร้างที่ไม่ได้ตรงตามมาตรฐานกำหนด ให้ทำการแก้ไข โดยปฏิบัติตาม คู่มือการซ่อมบำรุงทางหลวงท้องถิ่น กรมทางหลวงชนบท กระทรวงคมนาคม เท่านั้น

ห้ามกระทำการแก้ไขด้วยวิธีหดยอดยางโดยเด็ดขาด


การทดสอบความรู้ทางอรรถปริยัติของแม่แห่งตัวอย่างคนในกฐิต

1. กำลั้ดัดปุ้ปุระลัยของแ่งทัวอัยงักอนกรัถที่อัย 28 วัน ต้องเึนอัยกัว่า 280 กก./ตร.ซม. หรือตานิที่เึนบกักำหนด ถ้าแ่งทัวอัยงักอนกรัถเึนกำลั้ดัดทักัว่าทักักำหนด กำลั้ดัดอัยลัยทัง 3 ของทัวอัยงักต้องลั้กัว่าทักักำหนดเึนอัยกัว่าร้อลัละ 5 และผลตังของอัยงักอัยทังลั้ดัดอัยลัยคองอัยลั้ดัดอัยคักัว่าทักักำหนดอัยลัละ 10

2. หากปรากฏว่าค่าเฉลี่ยของแฟงตัวอย่างคอนกรีตดังกล่าวต่ำกว่า 280 กก./ตร.ซม. หรือตมที่แบบกำหนด ผู้รับจ้างมีสิทธิ์ที่จะขอให้ทำการตรวจสอบค่าความต้านทานแรงอัดของคอนกรีตในช่วงงานนั้นๆเพิ่มเติมโดยการเจาะเก็บตัวอย่างงานตามมาตรฐาน งานผิวจราจรแบบคอนกรีต มทก.231-2562 ของกรมทางหลวงชนบท กระทรวงคมนาคม และนำไปทดสอบในห้องปฏิบัติการ ตม มทก.(ท)105.1 การเจาะเก็บตัวอย่างทดสอบต้องดำเนินการภายใน 60 วัน นับจากวันที่เทคอนกรีตช่วงนั้นๆ โดยผู้รับจ้างจะต้องเป็นผู้รับผิดชอบค่าใช้จ่ายในการดำเนินการทั้งสิ้น สำหรับตำแหน่งที่เจาะและจำนวนตัวอย่างที่ต้องการ ผู้ควบคุมงานจะเป็นผู้กำหนด

รายละเอียดตามหลัก DOWEL BAR SR 24 RB 19 มม. ยาว 50 ซม. @ 50 ซม. C/C ให้เหล็ก 10 ท่อนต่อ 1 รอยต่อ @ 5 เมตร  
 สำหรับขยายขอบบริเวณแปลนหน้า ส่วนรอยต่อเพื่อการขยายตัวให้ก่อสร้างด้วยเหล็ก DOWEL BAR SD 40 DB 16 มม. ยาว 50 ซม. @ 0.50 เมตร C/C ให้เหล็ก 10 ท่อน 1 ช่วงรอยต่อ @ 5 เมตร  
 WIERD MESH Ø 4 มม. @ 0.20 เมตร # ตามการตั้งรับรูป

ลงสู่รางใต้ทางตามสภาพของบริเวณที่กำหนด

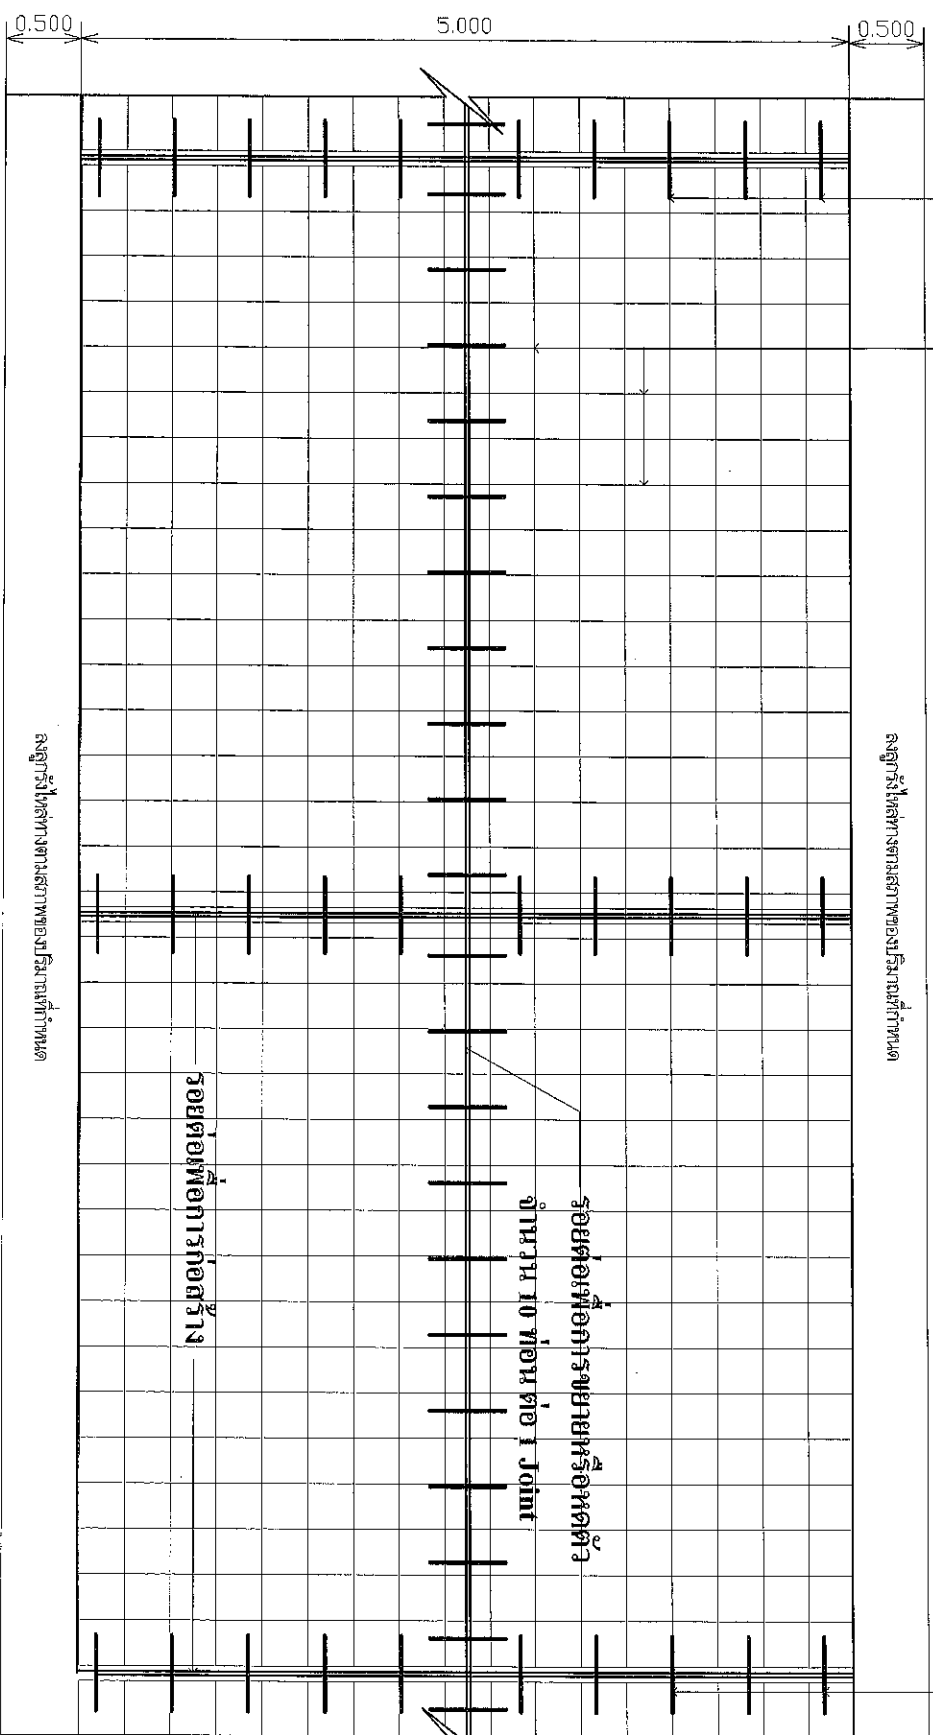

ลงสู่รางใต้ทางตามสภาพของบริเวณที่กำหนด

รอยต่อเพื่อการก่อสร้าง

รอยต่อเพื่อการขยายหรือหดตัว  
 จำนวน 10 ท่อนต่อ 1 Joint

5.000

5.000

รูปแบบผิวจราจรคอนกรีต 1:50

กองช่าง

องค์การบริหารส่วนตำบลหัวเขา

เขียนแบบ / สักรวช

ผู้ช่วยนายช่างโยธา

นายอินัน สร้อยระย้า

เขียนแบบ / สักรวช

นางสาวกัญฐ์ รอดทอง

นายช่างโยธานาถงาน

ตรวจสถาป

นายสุวิทย์ ฟูสุขุมวณ

นายช่างโยธานาถงาน

จำเอก

นางพ. เกษประทุม

ปลัดองค์การบริหารส่วนตำบล

อนุมัติ

นายอินัน พงษ์รอด

นายกองค์การบริหารส่วนตำบลหัวเขา

แบบวิศวกรรม

ก่อสร้างถนน 4.5 ม. 4 นิ้ว 4 นิ้ว

ใบสั่ง


- รูปแปลนผิวจราจรคอนกรีต

จำนวนที่ 9/11

หมายเลข


မှတ်ချက်

- ถ้ามีคณะกรรมการอยู่จริงในพื้นที่ชุมชนไม่ผ่านแน่
- ระดับให้ใช้ระดับถนน คลสธ./ลาดยางเดิมตามสภาพเป็นระดับเดียวกับตามสภาพ หากมีไม่ดีกว่าหนึ่ง
- ให้ผู้รับจ้างลงสู่ทางลาดต่อจากคอนกรีตที่ก่อสร้าง (จุดสิ้นสุดโครงการ) ของวงกลมวงถนน คลสธ. ยาวไปอีก 3 เมตร (กรณีจุดสิ้นสุดต่อยับถนน คลสธ. ก็ใช้ได้ลง)
- ให้เพิ่มลูกปูนหากครั้งที่เทคอนกรีตอย่างน้อย 2 ชุดละ 3 เมตรตัวอย่าง (ทดสอบลูกปูนที่อายุ 28 วัน = 280 ksc. ทรงลูกปากก็เมตร) ส่วนยุบคอนกรีต (SLUMP) ไม่มากกว่า 7.5  $\pm$  2.5 ซม.
- โดยผู้รับจ้างจะต้องจัดหาเครื่องมือทดสอบ หากความถูกต้อง (SLUMP) และแบบหล่อแบ่งคอนกรีต ตามที่กำหนดประจำไว้ที่หน้างานให้เพียงพอ
- ให้ผู้รับจ้างดำเนินการวางแป้นทดสอบ (ขนาดแป) ทั้งสองข้างทางยาวตลอดสายที่ยกก่อสร้าง พื้นที่ไม่น้อยกว่า 300 ตารางเมตร
- ให้ผู้รับจ้างชุดที่หนึ่งทางเดิม (ลูกรัง) ลึก 0.10 เมตร กว้างไม่น้อยกว่า 6.00 เมตรยาวตลอดสายที่จะทำการก่อสร้าง หรือมีพื้นที่รวมกันไม่น้อยกว่า 1,800 ตารางเมตร
- ผลทดสอบค่ากำลังอัดลูกรังที่หนึ่งทางใหม่ (ยกกระเบื้องหนา 0.30 เมตร) ให้เข้าเป็นเนื้อเดียวกัน โดยใช้ลูกขี้ผึ้งมาชั่งไม่น้อยกว่า 810 ลูกบาศก์เมตร (คิวหลวม)
- ปริมาณลูกรังที่หนึ่งทาง ยาวตลอดสาย สองด้านที่ก่อสร้างโดยใช้ปริมาณลูกรังตามที่กำหนดไม่น้อยกว่า 80 ลูกบาศก์เมตร (คิวหลวม)
- รายละเอียดของแบบทางมาตรฐานส่วนนี้ชี้แจงให้ผู้รับจ้างเป็นเกณฑ์หรือแบบมีการตั้งแย่งให้ชัดเจนขึ้นของผู้ควบคุมงาน
- \*\*\* การทดสอบค่าความหนาแน่นของการบดที่บดในถนน ทนดินละ ไม่เกิน 15 ซม.
- การทดสอบค่ากำลังอัดและแรงขยี้ของคอนกรีต ผู้ควบคุมงาน จะเป็นผู้กำหนดเลือก ช่วงและวันที่เท หากพิจารณาแล้วว่า แบ่งตัวอย่างชุดใด อายุใกล้ครบ 28 วัน จะทำการวางขยี้ทดสอบ โดยแบ่งเป็นตัวอย่างของการสุ่มสุ่ม และนำผลทดสอบไปคำนวณค่าความหนาแน่น

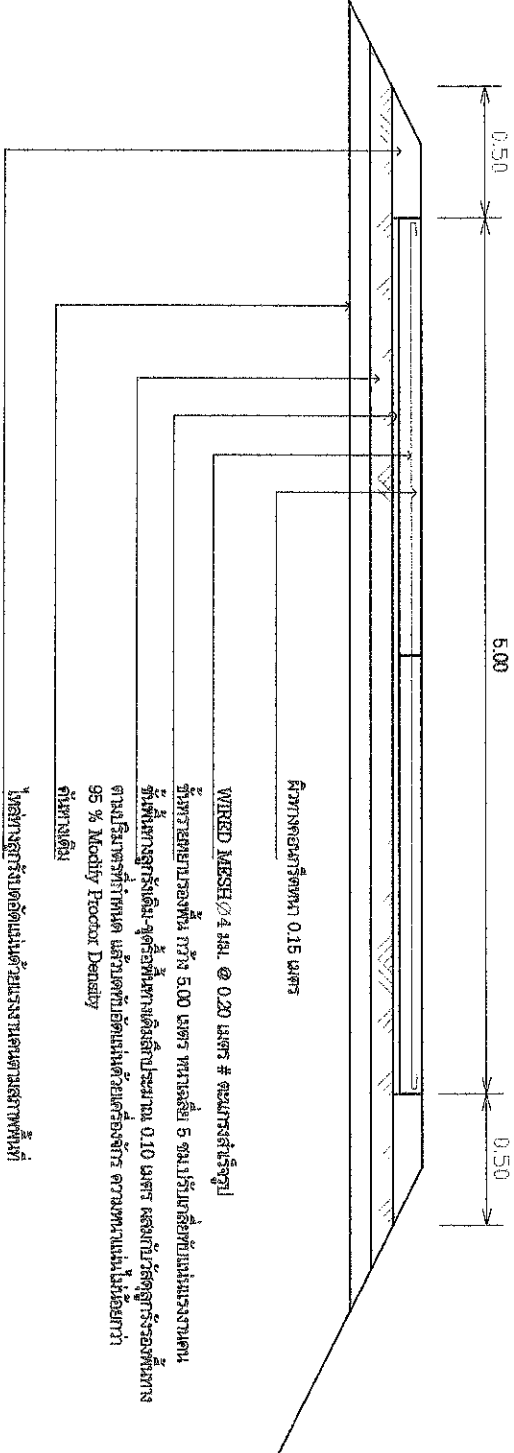


รูปตัดถนนผิวจราจรคอนกรีตเสริมเหล็ก มาตรฐาน 1 : 50

|         |   |
|---------|---|
| กองช่าง | <p>องค์การบริหารส่วนตำบลหนองขา</p> <p>เขียนแบบ / สำรวจ</p> <p>นายไธสง ศรีอยู่ช่วย<br/>ผู้ควบคุมช่างโยธา</p> <p>เขียนแบบ / สำรวจ<br/>Jfucn,</p> <p>นางสาวสุณัฐ รอดทอง<br/>นางช่างโยธาชำนาญงาน</p> <p>ตรวจข้อบ<br/>นายสุวิทย์ บุตรสุวรรณ<br/>นายช่างโยธาชำนาญงาน</p> <p>เห็นชอบ<br/>จ่าอา<br/>นภาพ ภาณุประทุน<br/>ปลัดองค์การบริหารส่วนตำบล</p> <p>อนุมัติ<br/>นายอนุ ทองสงค์<br/>นายกองค์การบริหารส่วนตำบลหนองขา</p> <p>แบบโครงการ</p> <p>ก่อสร้างถนน อ.ส.ล. หมู่ 4 บ้านโคกไทร</p> <p>เปิดซอง</p> <p>- จ้างดำเนินการสำรวจหาขอบเขตที่ดินเพื่อสร้าง</p> <p>จำนวนที่ 10/11</p> <p>ทรงายเหตุ</p> |
|---------|---|

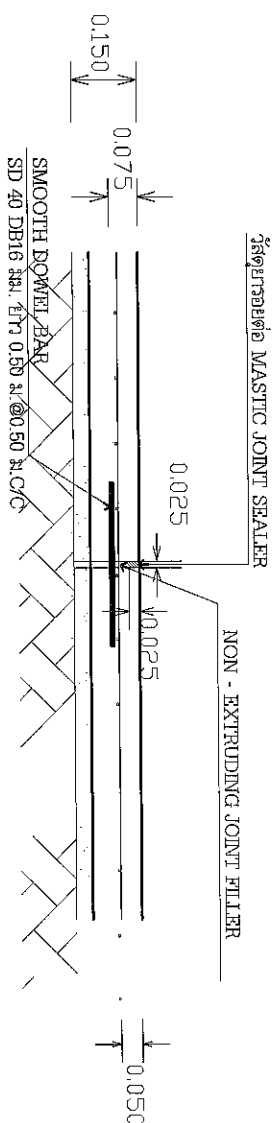

ขยายรอยต่อ EXPANSION JOINT : NOT TO SCALE

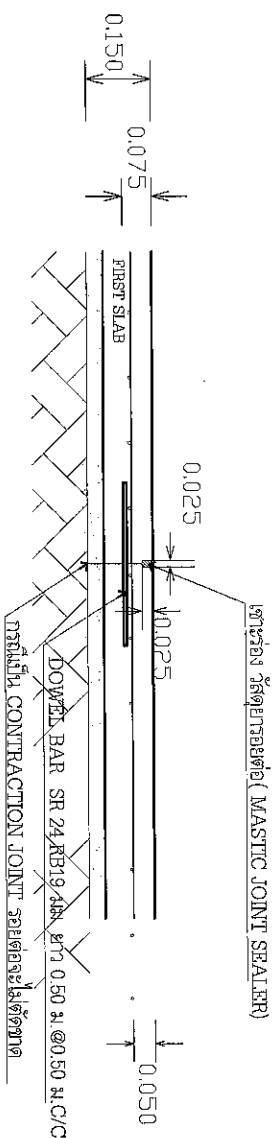

ขยายรอยต่อ CONSTRUCTION JOINT AND CONTRACTION : NOT TO SCALE

## หมายเหตุ รอยต่อคอนกรีต

- ให้ผู้รับจ้างวางแผนให้พร้อมรอยต่อถนนเดิมพร้อมหยดยาง (ไม่ต้องงะละเล็กละหลึก) ตามแบบขยายต่อ
- เพื่อการขยายตัวได้ ให้ใช้เสริมเหล็กท้ายสุดของถนนหรือจุดสิ้นสุดโครงการให้เป็นไปตามรอยต่อเพื่อ
- การก่อสร้างคงต่อไป ซึ่งหากเป็นจุดสิ้นสุดถนนจะต้องใส่เหล็ก

|                                                             |  |
|-------------------------------------------------------------|--|
| กองช่าง                                                     |  |
| องค์การบริหารส่วนตำบลหัวเขา                                 |  |
| เขียนแบบ / สุวิวิจ                                          |  |
| นายโยธิน สร้อยระย้า<br>ผู้ช่วยนางช่างโยธา                   |  |
| เขียนแบบ / สุวิวิจ                                          |  |
| นางสาวศุภากร วรทอง<br>นายช่างโยธาชำนาญงาน                   |  |
| ตรวจสอบ                                                     |  |
| นายอัมรินทร์ นุศลธรรม<br>นายช่างโยธาชำนาญงาน                |  |
| เขียนสอบ                                                    |  |
| จำเอก                                                       |  |
| นางนพ เกษมประทุม<br>ปลัดองค์การบริหารส่วนตำบล               |  |
| อนุมัติ                                                     |  |
| นายธน พงษ์รอด<br>นายกองค์การบริหารส่วนตำบลหัวเขา            |  |
| แบบโครงสร้าง                                                |  |
| ก่อสร้างตามค.ส.ท.ม. 4 บ้านวัดไทร                            |  |
| ไม่ติด                                                      |  |
| - รอยต่อเพื่อการก่อสร้าง<br>- รอยต่อเพื่อการขยายตัว (ถ้ามี) |  |
| จำนวนที่ 11/11                                              |  |
| หมายเหตุ                                                    |  |