

# โครงการก่อสร้างถนนคอนกรีตเสริมเหล็ก หมู่ที่ 4 บ้านวัดไทร

สถานที่ดำเนินการ ช่วงที่ 1 เริ่มต้นที่ถนนสายคันคลองส่งน้ำ 6 ซ้าย ม.-อ.(ฝั่งขวา) บริเวณที่นา

นางสาวสุวรรณา คหะรักษ์ ถึง บริเวณบ้านพักชลประทาน

ช่วงที่ 2 เริ่มต้นจากบริเวณบ้านพักชลประทาน ถึงสิ้นสุด ถนนสายคันคลอง


ส่งน้ำมะขามเต่า-กระเสี้ยว(ฝั่งซ้าย) บริเวณที่นาทางจันทร์เพ็ญ นาทิพย์

ปริมาณงาน ช่วงที่ 1 กว้าง 6.00 เมตร ยาวรวม 546 เมตร หนา 0.15 เมตร มีพื้นที่ไม่น้อยกว่า 3,276 ตารางเมตร

ช่วงที่ 2 กว้าง 5.00 เมตร ยาวรวม 224 เมตร หนา 0.15 เมตร มีพื้นที่ไม่น้อยกว่า 1,120 ตารางเมตร

พร้อมถนนคู่ข้าง ค.ส.ท.หนา 0.15 เมตร มีพื้นที่ไม่น้อยกว่า 154 ตารางเมตร โดยมีพื้นที่ถนน

รวมกันไม่น้อยกว่า 4,550 ตารางเมตร รายละเอียดตามที่แบบกำหนด

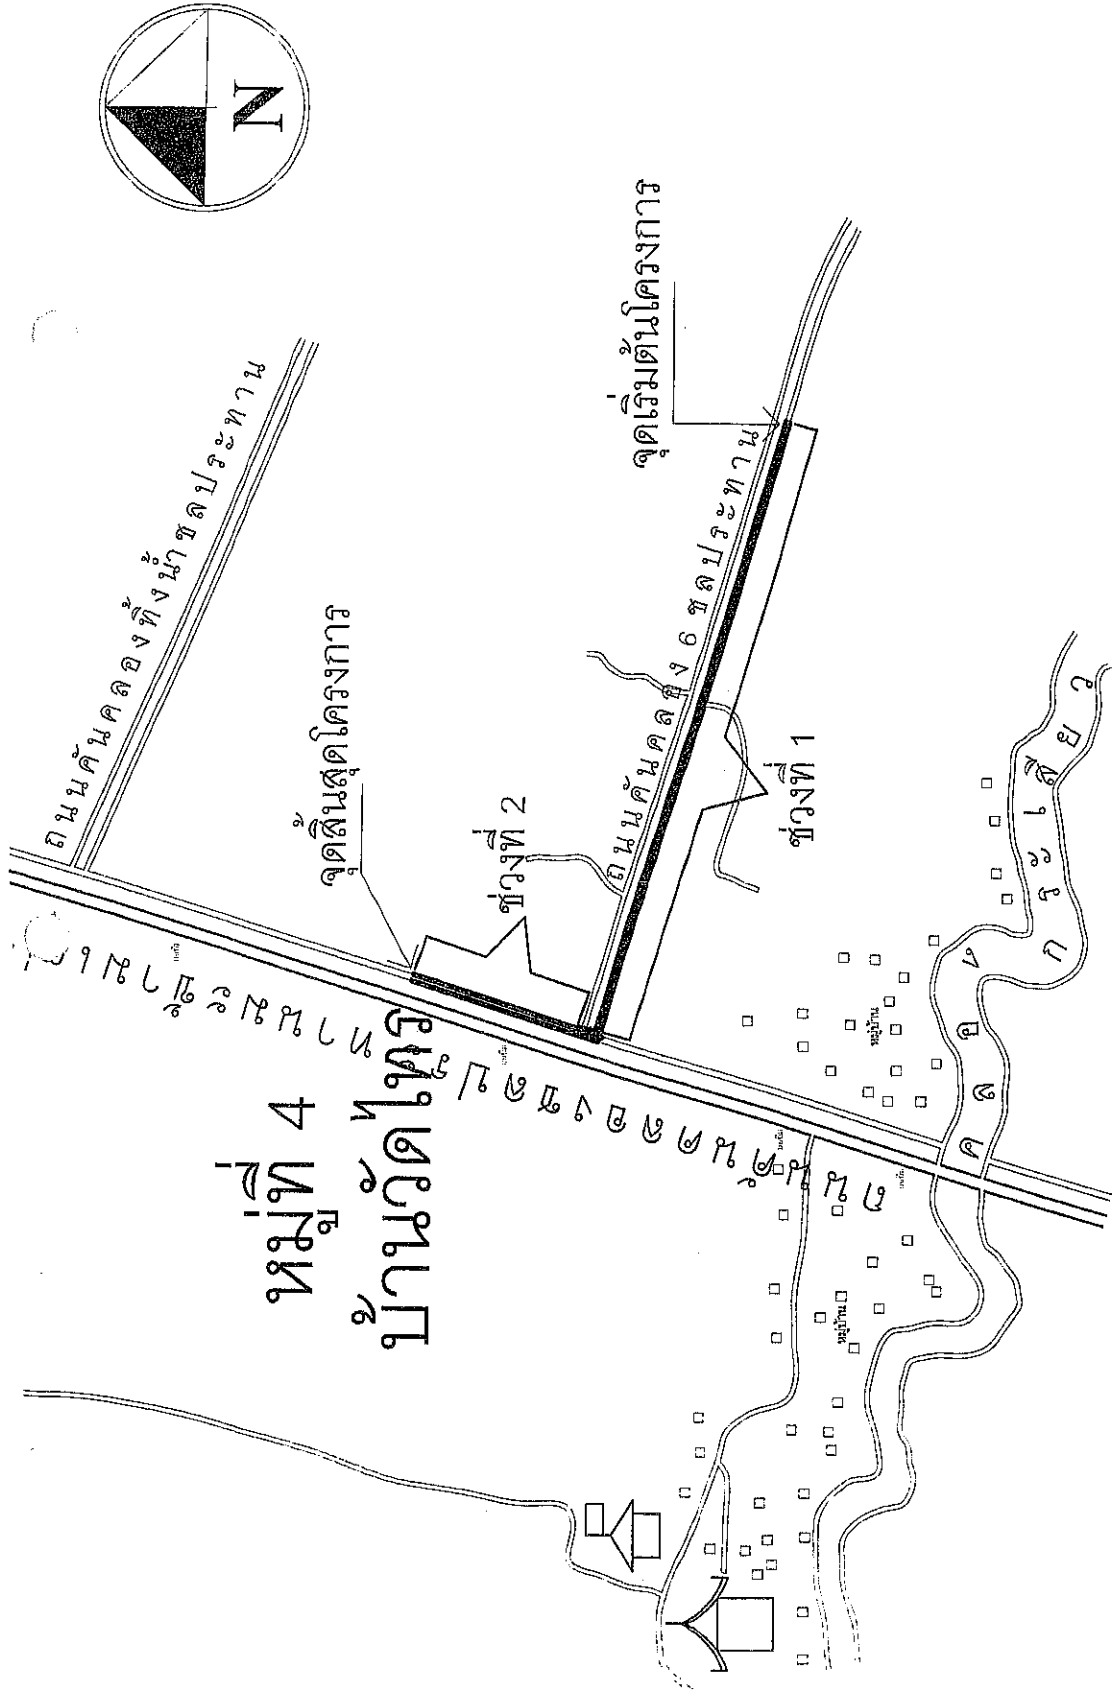

สถานที่ดำเนินการ ช่วงที่ 1 เริ่มต้นที่ถนนสายคันคลองส่งน้ำ 6 ซ้าย ม.-อ. (ฝั่งขวา) บริเวณที่นา  
 นางสาวสุวรรณา คन्हักษ์ ถึง บริเวณบ้านพักชลประทาน  
 ช่วงที่ 2 เริ่มต้นจากบริเวณบ้านพักชลประทาน ถึงสิ้นสุด ถนนสายคันคลอง  
 ส่งน้ำมะขามเฒ่า-กระเสี้ยว (ฝั่งซ้าย) บริเวณที่นาทางจันทร์เพ็ญ น้ำทิพย์

ผังบริเวณสถานที่ดำเนินการ

|                                                      |
|------------------------------------------------------|
| กองช่าง                                              |
| องค์การบริหารส่วนตำบลหัวเขา                          |
| ตำราจ/เขียนแบบ                                       |
| นายโยธิน สร้อยระย้า<br>ผู้ช่วยนายช่างโยธา            |
| สำราจ/เขียนแบบ                                       |
| นางสาวศุภมาส รอดทอง<br>นายช่างโยธาชำนาญงาน           |
| ตรวจ/ผู้ตรวจ                                         |
| นายสุรชัย จันทะสิงห์<br>ผู้อำนวยการกองช่าง           |
| เห็นชอบ                                              |
| นายก อบจ. ประจวบ<br>ปลัดองค์การบริหารส่วนตำบล        |
| อนุมัติ                                              |
| นายธนู ทองรอด<br>นายกองค์การบริหารส่วนตำบลหัวเขา     |
| แบบโครงการ                                           |
| ก่อสร้างถนนคอนกรีตเสริมเหล็ก<br>หมู่ที่ 4 บ้านวัดไทย |
| แสดง                                                 |
| - แผนที่พอสั่งพิมพ์                                  |
| จำนวนแผ่นที่ 1/14                                    |
| วันที่ - มกราคม 2566                                 |

# ข้อกำหนดเฉพาะงานและรายการประกอบแบบ

## บทกำหนด ด้านวัสดุก่อสร้าง

### 1.วัสดุ กรวดทรายหรือดินและวัสดุคัดเลือกต่างๆ

- 1.1 ผู้รับจ้างต้องมีโรงงานชุดหรือลอก กรวด ทรายหรือดินในที่ดินกรรมสิทธิ์ หรือต้องมีเอกสารยินยอมให้ใช้ผลิตภัณฑ์จากโรงงานชุดหรือลอก กรวด ทรายหรือดินในที่ดินกรรมสิทธิ์ที่ไม่ใช่ของผู้ยื่นเสนอ
- 1.2 ผู้รับจ้างต้องมีสำเนาใบอนุญาตประกอบกิจการโรงงาน(แบบ ร.ง.4) จากกรมโรงงานอุตสาหกรรมของผู้รับจ้างหรือผู้ให้ความยินยอมใช้ผลิตภัณฑ์ ทั้งนี้ใบอนุญาตประกอบกิจการโรงงาน(แบบ ร.ง.4) จากกรมโรงงานอุตสาหกรรมต้องไม่หมดอายุ ถูกสั่งพักใช้ หรือเพิกถอน
- 1.3 กรณีไม่มีใบอนุญาตประกอบกิจการโรงงาน(แบบ ร.ง.4) จากกรมโรงงานอุตสาหกรรมให้ใช้หนังสือรับรองการตั้งหน่วยงานผลิตการชุดหรือลอก กรวด ทรายหรือดินในที่ดินกรรมสิทธิ์สำหรับหน่วยงานก่อสร้าง จากหน่วยงานอุตสาหกรรมของผู้รับจ้าง หรือผู้ให้ความยินยอมใช้ผลิตภัณฑ์ ทั้งนี้หนังสือรับรองดังกล่าวต้องไม่หมดอายุ ถูกสั่งพักใช้หรือเพิกถอน

### 2. ปูนซีเมนต์และคอนกรีตผสมเสร็จ

- 2.1 ปูนซีเมนต์(สำหรับงานวางท่อ งานคอนกรีตโครงสร้างอื่นๆ)ที่ใช้ ต้องมีคุณสมบัติถูกต้องตามมาตรฐานผลิตภัณฑ์อุตสาหกรรมปูนซีเมนต์ปอร์ตแลนด์ มอก.15 ปูนซีเมนต์ที่ใช้ อาจบรรจุอยู่ในไซโล หรือเป็นแบบบรรจุถุงก็ได้ ถ้าเป็นแบบบรรจุถุง ผู้รับจ้างจะต้องจัดทำโรงเก็บปูน ปูนซีเมนต์ที่เหมาะสม เพื่อป้องกันไม่ให้ปูนซีเมนต์ชื้น ห้ามนำปูนซีเมนต์ที่จับตัวเป็นก้อนไปใช้งาน ปูนซีเมนต์ที่ใช้ตลอดงานตามสัญญาต้องเป็นตราและประเภทเดียวกัน เว้นแต่จะได้รับความเห็นชอบจากคณะกรรมการตรวจรับวัสดุ และผู้ควบคุมงานเป็นอย่างอื่น
- 2.2 คอนกรีตที่จะนำมาใช้เพื่อวางจากร จะต้องเป็นคอนกรีตผสมเสร็จ ตาม มอก.213-2553 ซึ่งผลผลิตโดย โรงงานผลิตคอนกรีตผสมเสร็จ(Concrete Batching Plant) ที่ได้มาตรฐาน โดยต้องมีระยะทางจากสถานที่ผสมเสร็จถึงสถานที่ตั้งโครงการ ที่ต้องถ่ายเทคอนกรีตออกจากโหมมตกภายในเวลา 1 ชั่วโมง 30 นาทีหลังจากเริ่มผสม ไม่นานกว่าให้ใช้คอนกรีตจากการผสมหรือไม่ผสมโดยเด็ดขาด ทั้งนี้ให้ผู้รับจ้างแสดงเอกสารรับรองการใช้ผลิตภัณฑ์จากโรงงานผสม และ อดราส่วนผสมคอนกรีต (Concrete Mix Design) ต่อผู้ว่าจ้างก่อนเข้าดำเนินการ เพื่อประกอบการพิจารณาอนุมัติใช้ และก่อนส่งมอบงานผู้รับจ้างจะต้องยื่นเอกสารจริงหรือเอกสารอื่นๆ ตามที่ผู้ควบคุมงานหรือคณะกรรมการอนุมัติพิจารณาแล้ว ของการใช้คอนกรีตผสมเสร็จที่ก่อสร้างทั้งหมดจากโรงงานผลิต เทียบปริมาณใกล้เคียง กับงานที่ก่อสร้าง(หรือมีใบจ่ายสินค้าซึ่งระบุชื่อโครงการ,กำลังอัด,หมายเลขทะเบียนรถ,วันและเวลาที่ผลิต)
- \*\*\*\*\* คอนกรีตที่นำมาใช้จะต้องเป็นคอนกรีตที่ผสมตามผลการออกแบบส่วนผสมคอนกรีตเท่านั้น ห้ามผู้รับจ้างเพิกถอนกรีตก่อนได้รับ การอนุมัติผลการออกแบบส่วนผสมคอนกรีตหรืออื่นๆ ถ้ามีโดยเด็ดขาด

|                                        |                                                           |                                                              |                                                         |                                                                 |                                                             |                                                                    |                                          |                   |                      |  |
|----------------------------------------|-----------------------------------------------------------|--------------------------------------------------------------|---------------------------------------------------------|-----------------------------------------------------------------|-------------------------------------------------------------|--------------------------------------------------------------------|------------------------------------------|-------------------|----------------------|--|
| กองช่าง<br>องค์การบริหารส่วนตำบลห้วยขา | สำรวจ/เขียนแบบ<br>นายโยธิน ตรีสุขธำ<br>ผู้ช่วยนายช่างโยธา | สำรวจ/เขียนแบบ<br>นางสาวสุภาวดี อดทอง<br>นายช่างโยธาด้านโยธา | ตรวจวัด<br>นายสุวิทย์ จันทวีเรือง<br>ผู้อำนวยการกองช่าง | เห็นชอบ<br>จ.เขต<br>นายพ เกษประทุม<br>ปลัดองค์การบริหารส่วนตำบล | อนุมัติ<br>นายธนู ทองรอด<br>นายกองค์การบริหารส่วนตำบลห้วยขา | แบบโครงการ<br>ก่อสร้างถนนคอนกรีตเสริมเหล็ก<br>หมู่ที่ 4 บ้านวัดไทร | แสดง<br>มาตราฐาน ม.ว.จ.ว. ราชบัณฑิตยสถาน | จำนวนแผ่นที่ 2/14 | วันที่ - มกราคม 2566 |  |
|----------------------------------------|-----------------------------------------------------------|--------------------------------------------------------------|---------------------------------------------------------|-----------------------------------------------------------------|-------------------------------------------------------------|--------------------------------------------------------------------|------------------------------------------|-------------------|----------------------|--|

# ข้อกำหนดเฉพาะงานและรายการประกอบแบบ

## บทกำหนด ด้านวัสดุก่อสร้าง(ต่อ)

### 3. การใช้วัสดุที่ผลิตภายในประเทศ

3.1 ให้ผู้รับจ้าง(คู่สัญญาของรัฐ) ใช้วัสดุประเภทวัสดุหรือครุภัณฑ์ที่จะใช้ในงานก่อสร้างเป็นวัสดุที่ผลิตภายในประเทศ โดยต้องใช้น้อยกว่า ร้อยละ 60 ของมูลค่าวัสดุที่จะใช้ในงานก่อสร้างทั้งหมดตามสัญญา โดยก่อนส่งมอบงานให้แสดงรายการใช้วัสดุภายในประเทศ เสนอให้ประธานกรรมการตรวจรับวัสดุ ตรวจสอบและพิจารณาเท่านั้น

3.2 ให้ผู้รับจ้างต้องให้หลักที่ผลิตภายในประเทศ ไม่น้อยกว่าร้อยละ 90 ของปริมาณเหล็กที่ใช้ทั้งหมดตามสัญญา โดยก่อนส่งมอบงานให้แสดงรายการใช้วัสดุภายในประเทศ เสนอให้ประธานกรรมการตรวจรับวัสดุ ตรวจสอบและพิจารณาเท่านั้น

### 4. การเก็บตัวอย่าง เพื่อตรวจสอบคุณภาพวัสดุก่อสร้าง

4.1 วัสดุทุกชนิดที่นำมาใช้งาน ต้องผ่านการตรวจสอบคุณภาพและได้รับการรับรองคุณภาพว่าได้ วัสดุที่ผู้รับจ้างนำมาใช้งานโดยพลการ ซึ่งไม่ได้การรับรองคุณภาพถือว่าเป็นวัสดุที่ไม่ได้ และจะไม่มีการจ่ายค่าเสียหายใดๆทั้งสิ้น การเก็บตัวอย่างเพื่อการตรวจสอบคุณภาพ ทั้งวิธีการเก็บและปริมาณตัวอย่างที่ใช้ให้เป็นไปตามที่กำหนดการเก็บตัวอย่างต้องมีตัวแทนของผู้จ้างร่วมทำการเก็บด้วยทุกครั้ง และทำหน้าที่ในการส่งตัวอย่างไปยังห้องปฏิบัติการทดลองของหน่วยงานที่เกี่ยวข้องได้ โดยค่าใช้จ่ายเกี่ยวกับการเก็บและส่งตัวอย่างเป็นภาระของผู้รับจ้างทั้งสิ้น และผู้จ้างจะไม่รับผิดชอบใดๆ ต่อความเสียหายที่เกิดขึ้นแก่ตัวอย่างที่ส่งตรวจสอบ

### 4.2 การเก็บแบ่งคอนกรีตจากสนาม และการทดสอบหาความต้านทานแรงอัดในห้องปฏิบัติการทดลอง

ในระหว่างทำการเทคอนกรีตทุกวันและทุกส่วนของโครงสร้างที่แตกต่างกัน ผู้ควบคุมงานจะเก็บตัวอย่างคอนกรีตโดยให้ผู้รับจ้างหล่อแ่งตัวอย่าง เพื่อเก็บไว้ทดสอบหาความต้านทานแรงอัดของคอนกรีต และวิธีการรับแบ่งคอนกรีตจะต้องให้มีสภาพใกล้เคียงกับวิธีการบ่มคอนกรีตในสนาม

4.2.1 ผู้รับจ้างต้องจัดหาเครื่องมือทดสอบหาความยุบตัว(SLUMP) และแบบหล่อแ่งคอนกรีตตามที่กำหนดประจำไว้ที่หน้างานให้เพียงพอ คอนกรีตสุดท้ายทำการทดสอบหาความยุบตัว(SLUMP) ทุกครั้งที่ผู้ควบคุมงานเห็นสมควรและอย่างน้อยที่สุดต้องทำการทดสอบ 1 ครั้งต่อการผลิตคอนกรีต 50 ลูกบาศก์เมตร โดยทำการทดสอบเมื่อเริ่มเทคอนกรีตและทุกครั้งที่มีการหล่อแ่งคอนกรีตด้วยอย่าง หากไม่มีเครื่องมือทดสอบหรือไม่ได้เก็บตัวอย่างหรือทดสอบ (ผู้ควบคุมงานอาจพิจารณาตรวจสอบเก็บห้ทำงานจริงที่เทคอนกรีตแล้วผู้รับจ้างต้องรับผิดชอบค่าใช้จ่ายเอง) โดยค่าความยุบตัว(SLUMP) ให้ใช้ 7.5 ซม. บวกลบ 2.5 ซม.

4.2.2 การเก็บตัวอย่างสำหรับทดสอบหาความต้านทานแรงอัดของคอนกรีต ซึ่งทำการเทในแต่ละวันจะต้องเก็บไม่น้อยกว่าวันละ 1 ครั้ง หรือน้อยกว่า 1 ครั้งต่อการผลิตคอนกรีต 120 ลูกบาศก์เมตรหรือไม่น้อยกว่า 1 ครั้งต่อคอนกรีตที่ใช้เทพื้น หรือหล่อผนังทุกพื้นที่ 450 ตารางเมตร หรือน้อยกว่า 1 ครั้งต่อคอนกรีตที่เทพื้นโครงสร้างแต่ละส่วน การหล่อแ่งตัวอย่างคอนกรีต ผู้รับจ้างจะต้องดำเนินการเอง และบ่มแ่งตัวอย่างทุกแ่งให้ลงรายละเอียด วัน เดือน ปี ที่หล่อ ชื่อผู้รับจ้าง ชื่องานก่อสร้าง และส่วนของโครงสร้างให้ชัดเจน เช่น STA.กม.ที่เท่าไร โดยใช้วัสดุมีคมเขียนลงบนแ่งของคอนกรีต ขณะที่ยังไม่แข็งตัว และต้องรองจนครบ 24 ชั่วโมง จึงถอดแบบและรับส่งให้ผู้ควบคุมงานโดยด่วน

|                                        |   |   |   |   |   |                                                                     |                                               |                   |                      |
|----------------------------------------|---|---|---|---|---|---------------------------------------------------------------------|-----------------------------------------------|-------------------|----------------------|
| กองช่าง<br>องค์การบริหารส่วนตำบลห้วยขา | สำรวจ/เขียนแบบ<br><br>นายโน้ตวัน ศรีสุกุล<br>ผู้ช่วยนายช่างโยธา | สำรวจ/เขียนแบบ<br><br>นางสาวรุ่งนัฐ รอดทอง<br>นายช่างโยธานางงาน | ตรวจรับ<br><br>นายณัฐชัย ศรีทอง<br>ผู้อำนวยการกองช่าง | เขียน<br><br>นางพ ภาณุประทุม<br>ปลัดองค์การบริหารส่วนตำบล | อนุมัติ<br><br>นายณัฐ ทองรอด<br>นายกองค์การบริหารส่วนตำบลห้วยขา | แบบ/โครงการ<br>ก่อสร้างงานซ่อมบำรุงเดิมเหล็ก<br>หน้าถ้ำ 4 บ้างใต้โพ | แสดง<br>- ข้อกำหนดพิเศษ<br>และรายการประกอบแบบ | จำนวนแผ่นที่ 3/14 | วันที่ - มกราคม 2566 |
|----------------------------------------|---|---|---|---|---|---------------------------------------------------------------------|-----------------------------------------------|-------------------|----------------------|

# ข้อกำหนดเฉพาะงานและรายการประกอบแบบ

## ขอบข่ายของสัญญาจ้าง

- เมื่อองค์การบริหารส่วนตำบลห้วยเขา ได้ส่งมอบพื้นที่ให้ผู้รับจ้างแล้ว ผู้รับจ้างจะต้องดำเนินการก่อสร้างให้แล้วเสร็จตามสัญญาที่กำหนดไว้ ส่วนพื้นที่ที่มีปัญหาและอุปสรรค องค์การบริหารส่วนตำบลห้วยเขา ขอสงวนสิทธิ์ในการตัด - เพิ่ม - ลดเนืองาน หรือแก้ไขสัญญาได้
- งานก่อสร้างตามสัญญาจ้างต้องเป็นไปตามรูปแบบ และรายการก่อสร้าง ซึ่งผู้ว่าจ้างและผู้รับจ้างได้ลงลายมือชื่อในฐานคู่สัญญาและยอมรับเป็นส่วนหนึ่งของสัญญาจ้าง
- ผู้รับจ้างรับว่าได้ตรวจดูสถานที่ก่อสร้าง รายละเอียดเยี่ยตสัญญา ข้อกำหนดพิเศษต่างๆ รวมทั้งรูปแบบและรายการก่อสร้างทุกฉบับโดยตลอด และเข้าใจความหมายโดยแจ้งชัดแล้ว จะแสดงการไม่รับรู้สภาพใดๆ อันเกี่ยวเนื่องกับการปฏิบัติงานตามสัญญาไม่ได้
- หากมีงานส่วนหนึ่งส่วนใดที่ไม่ปรากฏในแบบ แต่จำเป็นต้องเพิ่มเติมให้งานบรรลุตามวัตถุประสงค์และถูกต้องตามหลักวิชาช่างที่ดีให้ผู้รับจ้างดำเนินการในส่วนนั้น ตามคำแนะนำของผู้ควบคุมงาน โดยเคร่งครัดเพื่อให้งานบรรลุตามวัตถุประสงค์โดยไม่คิดเป็นงานเพิ่ม และเอาเงินเพิ่มอีกแต่อย่างใด
- กรณีรูปแบบของหรือข้อขัดแย้งกับรายการให้ถือเอาการปฏิบัติงานที่ถือว่า โดยถือเอาคำตัดสินของผู้ว่าจ้างเป็นอันสิ้นสุด และผู้รับจ้างจะต้องยอมทำงานนั้นๆ ให้เสร็จเรียบร้อยโดยไม่คิดเอาเงินเพิ่มแต่อย่างใด
- สิ่งใดที่ไม่ได้กล่าวไว้ในรูปแบบหรือรายการแต่เป็นส่วนจำเป็นต่อการกระทำ เพื่อให้งานสำเร็จบริบูรณ์โดยรวดเร็วด้วยดี และถูกต้องตามหลักวิชาช่าง ให้ถือเป็นส่วนที่ผู้รับจ้างต้องดำเนินการด้วย โดยผู้รับจ้างจะต้องยอมทำงานนั้นๆ ให้โดยไม่คิดเอาเงินเพิ่มอีกแต่อย่างใด
- ผู้รับจ้างจะต้องเข้าใจปัญหาต่างๆ และรู้ถึงสภาพแวดล้อมของจริงที่มีอยู่เดิม ในบริเวณของสถานที่ก่อสร้างและบริเวณข้างเคียงตลอดจนต้องรับผิดชอบในการแก้ไข เคลื่อนย้าย หรือรื้อถอนให้ถูกต้องตามสภาพพื้นที่ที่แท้จริง จนสามารถเข้าไปดำเนินการปรับปรุงตามรูปแบบและรายการได้ตามวัตถุประสงค์
- รูปแบบ และรายการที่กำหนดให้ไว้เป็นเพียงแนวทางปฏิบัติเท่านั้นอาจเปลี่ยนแปลงตามความเหมาะสมและสอดคล้องกับสภาพที่จริง โดยได้ประโยชน์ใช้สอยเต็มที่ ซึ่งการออกแบบที่สร้างจริงนี้จะต้องมีปริมาณเท่ากันหรือมากกว่ารูปแบบรายการเดิม โดยผู้ว่าจ้างเป็นผู้ให้ความเห็นชอบ และไม่ถือเป็นการเปลี่ยนแปลงหรือเพิ่มเติมเนืองานตามรายการในสัญญาแต่อย่างใด
- ระยะต่าง ๆ ที่กำหนดไว้ในแบบหรือแผนผัง หากไม่สามารถดำเนินการได้ตามสภาพความเป็นจริงให้อยู่ในดุลยพินิจของผู้ควบคุมงานและคณะกรรมการตรวจรับพัสดุในการที่จะแก้ไข และเปลี่ยนแปลงได้ตามความเหมาะสม
- เนืองานที่กำหนดไว้หากมีเหลือเกินจากแผนที่ส่งขบที่ที่กำหนดไว้ยินยอมให้ก่อสร้างเข้าไปในทางร่วมทางแยกในถนนซอยบริเวณใกล้เคียงได้ โดยให้อยู่ในดุลยพินิจของผู้ควบคุมงานและคณะกรรมการตรวจรับพัสดุ

|                                                       |
|-------------------------------------------------------|
| กองช่าง                                               |
| องค์การบริหารส่วนตำบลห้วยเขา                          |
| สำรวจ/เขียนแบบ                                        |
| นายนิพนธ์ ศรีระชา<br>ผู้ช่วยนายช่างโยธา               |
| สำรวจ/เขียนแบบ                                        |
| นางสาวสุภาวดี รอดทอง<br>นายช่างโยธาชำนาญงาน           |
| ตรวจ/อนุมัติ                                          |
| นายสุวิทย์ จันทวีรุ่ง<br>ผู้อำนวยการกองช่าง           |
| เห็นชอบ                                               |
| นายสุวิทย์ จันทวีรุ่ง<br>ปลัดองค์การบริหารส่วนตำบล    |
| อนุมัติ                                               |
| นายสมิทธิ์ ทองรอด<br>นายกองค์การบริหารส่วนตำบลห้วยเขา |
| แบบ/โครงการ                                           |
| ก่อสร้างถนนคอนกรีตเสริมเหล็ก<br>หมู่ที่ 4 บ้านวัดไทร  |
| แสดง                                                  |
| - ข้อกำหนดพิกัด<br>และรายการประกอบแบบ                 |
| จำนวนแผ่นที่ 4/14                                     |
| วันที่ - มกราคม 2566                                  |



## ข้อกำหนดเฉพาะงานและรายการประกอบแบบ

### หน้าที่และความรับผิดชอบของผู้สัญญา (ต่อ)

8. ผู้รับจ้างจะต้องไม่เองงานทั้งหมดหรือบางส่วนแห่งสัญญาไปจ้างช่วงอีกต่อหนึ่ง โดยไม่ได้รับความยินยอมเป็นลายลักษณ์อักษรจากผู้ว่าจ้างก่อน ทั้งนี้นอกจากในกรณีที่มีสัญญาจะจัดระเบียบไว้เป็นอย่างอื่น ความยินยอมดังกล่าวนี้ไม่เป็นเหตุให้ ผู้รับจ้างหลุดพ้นจากความรับผิด หรือพ้นหน้าที่ตามสัญญา และผู้รับจ้างจะต้องรับผิดชอบต่อความผิด และความประมาทเลินเล่อของผู้รับจ้างช่วง หรือของตัวแทน หรือของลูกจ้างของผู้รับจ้างช่วงนั้น ทุกประการ
9. งานบกพร่องใดๆ ไม่ว่าเกิดจากฝีมือไม่ดี ใช้วัสดุที่ด้อยคุณภาพ ความเสียหายจากความไม่ระมัดระวังหรือเหตุอื่นใดที่พบว่ามิอยู่ก่อนการสิ้นสุดการรับประกันตามระยะเวลาในสัญญา ให้ถือว่าผู้รับจ้างได้ซ่อมแซมและให้ใหม่ โดยการทำและวัสดุที่ใช้ให้เป็นไปตามข้อกำหนด และรายการก่อสร้าง หรืออาจแก้ไขโดยวิธีอื่นใดในลักษณะที่ผู้ควบคุมงานและคณะกรรมการตรวจรับวัสดุเห็นชอบและอนุญาตให้ทำได้ ข้อกำหนดดังกล่าวนี้ให้มีผลบังคับอย่างสมบูรณ์ โดยไม่ต้องคำนึงถึงว่างานบกพร่องดังกล่าวข้างต้นนี้ได้ทำโดยที่ผู้ควบคุมงานได้รู้แล้ว และในกรณีที่เกิดอุบัติเหตุขึ้น เนื่องจากความบกพร่องของผู้รับจ้าง นอกจากผู้รับจ้างจะต้องเป็นผู้รับผิดชอบโดยสิ้นเชิงแต่ฝ่ายเดียว ในบรรดาความเสียหายที่เกิดขึ้นแล้ว ผู้ว่าจ้างอาจถือเป็นสาเหตุในการบอกเลิกสัญญาได้
10. วัสดุที่ใช้ทำการรื้อถอนที่อยู่ในสภาพดีและใช้งานได้ ผู้รับจ้างต้องขนย้ายวัสดุเหล่านั้นไปเก็บไว้ ณ สถานที่ ที่เจ้าหน้าที่ผู้ควบคุมงาน กำหนดให้ โดยไม่สามารถคิดค่าใช้จ่ายใดๆ จากผู้ว่าจ้างได้ทั้งสิ้น
11. เมื่อสิ้นสุดการปฏิบัติงานในแต่ละวัน ให้ผู้รับจ้างทำความสะอาดพื้นที่ก่อสร้างตลอดจนพื้นที่ที่เกี่ยวข้องให้อยู่ในสภาพสะอาดเรียบร้อย ปราศจากเศษวัสดุ หรือสิ่งปฏิกูลอื่นใด ที่อาจก่อให้เกิดอุบัติเหตุหรือเป็นเหตุแห่งความเดือดร้อนรำคาญของประชาชนในพื้นที่และผู้ใช้เส้นทางสัญจร
12. ให้ผู้รับจ้างจัดเตรียมภาพถ่ายสี แสดงขั้นตอนการทำงานของผู้รับจ้าง ประกอบไปด้วย ภาพถ่ายก่อนดำเนินการ ขนมะดำเนินการทุกขั้นตอนตามรายการสัญญาและมาตรฐานการก่อสร้าง และ หลังดำเนินการแล้วเสร็จสมบูรณ์ เพื่อเป็นเอกสารประกอบการส่งมอบงานจ้าง
13. ผู้รับจ้างต้องรับผิดชอบในการอำนวยความสะดวกและปลอดภัยแก่ประชาชนผู้ใช้ทางโดยเฉพาะในบริเวณพื้นที่และเส้นทางที่ได้รับมอบจากผู้ว่าจ้างไปดำเนินการแล้วตลอดเวลา โดยการจัดทำ จัดหา และติดตั้งสิ่งจำเป็นต่างๆ เกี่ยวกับการจราจร จะเป็นค่าใช้จ่ายของผู้รับจ้าง และในขณะทำงานผู้รับจ้างต้องบำรุงรักษาเส้นทางให้ใช้สัญจรได้สะดวกและปลอดภัยตลอดเวลากว่าที่งานก่อสร้างเป็นอุปสรรคต่อการสัญจรอาจเปิดให้รถเดินทางได้โดยผู้รับจ้างจะต้องจัดหาติดตั้ง อุปกรณ์ และเครื่องหมายความสัญญาณจราจร เตือนล่วงหน้าและป้องกันอุบัติเหตุ หากการสัญจรไม่สามารถมองเห็นในทิศทางตรงกันข้าม ผู้รับจ้างต้องให้มีพนักงานให้สัญญาณและจัดการจราจรให้ผ่านได้โดยสะดวกหากมีความจำเป็นต่อการเปิดการจราจรเป็นบางช่วงจะต้องได้รับอนุญาตจากผู้ควบคุมงานและผู้รับจ้างจะต้องจัดทำทางเบี่ยงให้การจราจรผ่านได้ตามปกติก่อนที่จะทำการปิดทางเพื่อทำการก่อสร้าง พร้อมทั้งมีการแนะนำและเตือนผู้ที่ใช้เส้นทางเบี่ยงหรือสะพานเบี่ยงให้ผู้รับจ้างต้องดูแลและบำรุงรักษาทางเบี่ยง หรือสะพานเบี่ยงให้อยู่ในสภาพที่ใช้งานได้ดี และสะดวกตลอดเวลาที่ใช้งาน

|                                        |   |   |   |   |   |                                                                     |                                                  |                   |                      |
|----------------------------------------|---|---|---|---|---|---------------------------------------------------------------------|--------------------------------------------------|-------------------|----------------------|
| กองช่าง<br>องค์การบริหารส่วนตำบลหัวเขา | สำรวจ/เขียนแบบ<br><br>นายณัฐกร ศรีสุภา<br>ผู้ช่วยนายช่างโยธา | สำรวจ/เขียนแบบ<br><br>นางสาวณัฐกร ศรีสุภา<br>นายช่างโยธาชำนาญงาน | ตรวจ/อนุมัติ<br><br>นายสุรชัย พันธ์เรือง<br>ผู้อำนวยการกองช่าง | เห็นชอบ<br><br>นางพ. เกษมธนา<br>ปลัดองค์การบริหารส่วนตำบล | อนุมัติ<br><br>นายธนู ทองรอด<br>นายกองค์การบริหารส่วนตำบลหัวเขา | แบบ/โครงการ<br>ก่อสร้างถนนคอนกรีตเสริมเหล็ก<br>หมู่ที่ 4 บ้านวัดไทร | แสดง<br>- ข้อกำหนดเฉพาะงาน<br>และรายการประกอบแบบ | จำนวนแผ่นที่ 6/14 | วันที่ - มกราคม 2566 |
|----------------------------------------|---|---|---|---|---|---------------------------------------------------------------------|--------------------------------------------------|-------------------|----------------------|

## ข้อกำหนดเฉพาะงานและรายการประกอบแบบ

### หน้าที่และความรับผิดชอบของคู่สัญญา (ต่อ)

14. การติดตั้งป้ายและสัญลักษณ์ควบคุมการจราจรในขณะทำงาน ผู้รับจ้างต้องจัดให้มีป้ายและสัญลักษณ์จราจร เพื่อเตือนและแนะนำให้ผู้ใช้ทางทราบล่วงหน้า ให้ผู้ใช้ยานพาหนะด้วยความระมัดระวังมิให้เกิดอุบัติเหตุขึ้นเนื่องมาจากการก่อสร้างกรณีที่ได้เป็นต้องปิดกั้นทางที่ใช้สัญจรตามปกติต้องจัดให้มีแผนกพร้อมป้าย หรือเครื่องหมายเตือนล่วงหน้า และในเวลากลางคืนต้องจัดให้มีแสงสว่างติดตั้งไว้ที่แผนกด้วยในบริเวณที่กำลังก่อสร้าง การกองวัสดุไว้บนเส้นทาง ต้องจัดให้มีป้ายเตือนเพิ่มเติมเป็นกรณีพิเศษตลอดเวลาทำงาน และถ้าเป็นงานที่ทำบริเวณทางตัดหรือทางแยก นอกจากจะต้องติดตั้งป้ายเตือนบริเวณก่อสร้างแล้วยังต้องติดตั้งบนทางตัดหรือทางแยกสายที่มีการจราจรผ่านบริเวณที่มีการก่อสร้างด้วยป้ายเครื่องหมายและสัญลักษณ์จราจรรวมทั้งการติดตั้ง จะต้องเป็นไปตามแบบมาตรฐาน และหากจำเป็นจะต้องจัดให้มีแสงสว่างสามารถเห็นลักษณะและรายละเอียดของป้ายเครื่องหมายได้ชัดเจน

### การควบคุมคุณภาพ การก่อสร้าง


1. การก่อสร้างหรือสิ่งที่ต้องดำเนินการนอกเหนือจากที่กำหนดให้ขึ้นไปตาม มาตรฐานงานทางของ-องค์กรบริหารส่วนตำบลหัวเขา พ.ศ.2566 (ถ้ามี)
2. คอนกรีตที่จะเท ต้องเทติดต่อกันโดยสม่ำเสมอให้เต็มแต่ละช่วง และมีความหนาที่จะแตงผิวได้ทันทีทุกครั้ง ห้ามหยุดเทคอนกรีตในแต่ละช่วงเป็นอันขาด หากมีเหตุขัดข้องใดๆ อันทำให้การเทคอนกรีตในแต่ละช่วงที่หยุดช่วงจะเกินกว่า 30 นาที จะต้องรื้อคอนกรีตที่เทแล้วในช่วงนั้นออกทิ้งเสียทั้งหมด หรือรับทำรอยต่อเนื่องจากการก่อสร้าง(Construction Joint) ที่จุดนั้นทันที แต่ถ้าเหตุขัดข้องนั้น หยุดชะงักนานไม่เกินกว่า ระยะเวลาที่กำหนด ตรงแนวคอนกรีตที่เทแล้วก็จะใหม่ ให้ใช้พลั่ว คลุกคอนกรีตเก่าและใหม่ผสมกัน
3. การวางเหล็กเสริม เหล็ก Dowels และ Tie Bars จะต้องมีขนาดและอยู่ในตำแหน่ง ที่ถูกต้องตามที่กำหนดไว้ในแบบแปลนทุกประการ ในกรณีวางตะแกรงเหล็กเสริม จะต้องแนบไว้จะไม่เกิดการทรุดตัวในขณะเทคอนกรีต เมื่อผูกเหล็กต่างๆ เสริมเรียบร้อยแล้ว ก่อนดำเนินการเทคอนกรีต ผู้รับจ้างต้องแจ้งให้ผู้ควบคุมงานตรวจสอบความเรียบร้อยของการผูกเหล็กและอื่น ๆ ก่อน
4. ก่อนดำเนินการเทคอนกรีตครั้งแรกให้ผู้รับจ้างแจ้งเจ้าหน้าที่ผู้ควบคุมงานทราบล่วงหน้าในวันและเวลาของการ อย่างน้อย 1-3 วัน เพื่อจะได้ประสานผู้ที่เกี่ยวข้อง เข้าทำการตรวจสอบ และมาตรวจการความพร้อมในการผสมคอนกรีต ระยะเวลาในการขนส่งคอนกรีตจากแหล่งผลิตคอนกรีต ถึงสถานที่ก่อสร้าง และมาตรวจการความพร้อมของเครื่องจักรขนส่งคอนกรีตระบบจราจร
5. ก่อนทำการเทคอนกรีตทุกครั้งให้ผู้รับจ้างแจ้งผู้ควบคุมงานล่วงหน้าอย่างน้อย 1 วัน เพื่อตรวจสอบ ระดับ จำนวน และขนาดของเหล็กเสริมคอนกรีตให้เป็นไปตามรูปแบบและรายการที่สัญญาจ้างกำหนดเสียก่อน หากผู้รับจ้างดำเนินการไปโดยพลະการ เจ้าหน้าที่ผู้ควบคุมงาน มีสิทธิสั่งให้รื้อ หรือแก้ไขใหม่ โดยผู้รับจ้างจะต้องยินยอมดำเนินการตาม โดยค่าวัสดุและค่าใช้จ่ายต่างๆ จากการรื้อถอนและแก้ไขใหม่ทั้งหมดที่เกิดขึ้น ให้เป็นภาระของผู้รับจ้างทั้งสิ้น และจะเรียกค่าใช้จ่ายและระยะเวลาที่เพิ่มขึ้นจากผู้ว่าจ้างอีกไม่ได้

|                                        |                                                           |                                                             |                                                               |                                                                 |                                                             |                                                                     |                                                  |                   |                      |
|----------------------------------------|-----------------------------------------------------------|-------------------------------------------------------------|---------------------------------------------------------------|-----------------------------------------------------------------|-------------------------------------------------------------|---------------------------------------------------------------------|--------------------------------------------------|-------------------|----------------------|
| กองช่าง<br>องค์การบริหารส่วนตำบลหัวเขา | สำรวจ/เขียนแบบ<br>นายเชษฐา ทรัพย์ธำ<br>ผู้ช่วยนายช่างโยธา | สำรวจ/เขียนแบบ<br>นางสาวศุภมาส รอดทอง<br>นายช่างโยธานานางาน | ตรวจ/เขียนแบบ<br>นายสุวิทย์ จันทรีเรือง<br>ผู้อำนวยการกองช่าง | เห็นชอบ<br>จันท<br>นายพ ภาณุประทุม<br>ปลัดองค์การบริหารส่วนตำบล | อนุมัติ<br>นายธนู ทองรอด<br>นายกองค์การบริหารส่วนตำบลหัวเขา | แบบ/โครงการ<br>ก่อสร้างถนนคอนกรีตเสริมเหล็ก<br>หมู่ที่ 4 บ้านวัดไทร | แสดง<br>- ติดกำหนดเฉพาะงาน<br>และรายการประกอบแบบ | จำนวนแผ่นที่ 7/14 | วันที่ - มกราคม 2566 |
|----------------------------------------|-----------------------------------------------------------|-------------------------------------------------------------|---------------------------------------------------------------|-----------------------------------------------------------------|-------------------------------------------------------------|---------------------------------------------------------------------|--------------------------------------------------|-------------------|----------------------|






|                              |                                                                |
|------------------------------|----------------------------------------------------------------|
| กองช่าง                      |                                                                |
| องค์การบริหารส่วนตำบลห้วยเขา |                                                                |
| เขียนแบบ / สำเนา             | นายโยธิน สร้อยระย้า<br>ผู้ช่วยนายกฯ อบจ.น่าน                   |
| เขียนแบบ / สำเนา             | นางสาวกัญญา รอดทอง<br>นายก อบจ.น่าน                            |
| ตรวจเช็ค                     | นายสุวิทย์ จันทะโรจ<br>ผู้อำนวยการกองช่าง                      |
| เห็นชอบ                      | นางพ. เกษประทุม<br>ปลัดองค์การบริหารส่วนตำบล                   |
| อนุมัติ                      | นายธนู ทองรอด<br>นายก อบจ.น่าน                                 |
| แบบโครงการ                   | ก่อสร้างถนนคอนกรีตเสริมเหล็ก<br>พื้นที่ 4 ไร่ 1 งาน 10 ตารางวา |
| แสดง                         | แปลนผิวจราจร กว้าง 6.00 เมตร                                   |
| จำนวนแผ่นที่                 | 9 / 14                                                         |
| วันที่                       | มกราคม 2566                                                    |
| หมายเหตุ                     |                                                                |

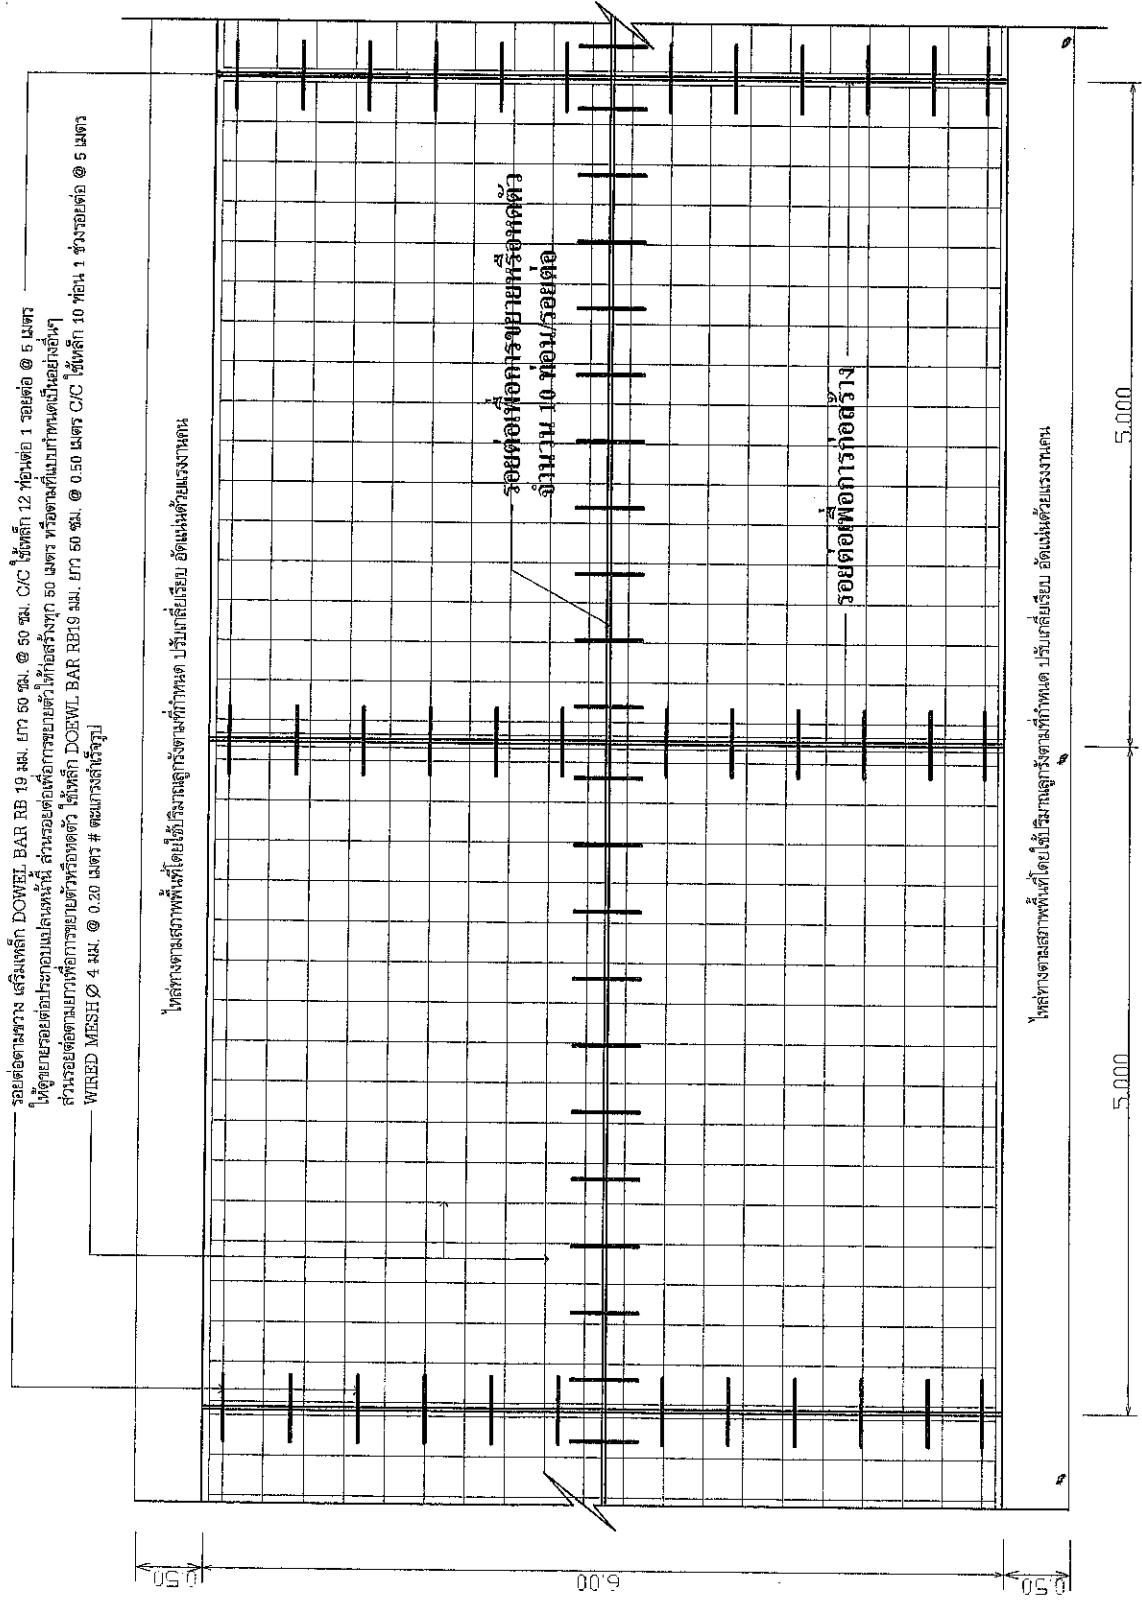

รูปแบบผิวจราจรคอนกรีต 1: 50

หมายเหตุ : ผิวจราจร กว้าง 6.00 เมตร ยาว 546 เมตร หนา 0.15 เมตร


- ลักษณะงานเป็นการสัญจรในพื้นที่ชุมชนไม่หนาแน่น
- ระดับให้ระดับถนน คลล./ลาดยางเดิมตามสภาพเป็นระดับเดียวกับตามสภาพ หากไม่ได้กำหนด
- ให้ผู้รับจ้างลงลูกรังทางลาดต่อจากคอนกรีตที่ก่อสร้าง(จุดสิ้นสุดโครงการ)ของควมกว้างถนน คลล.ยาวไปอีก 3 เมตร (กรณีจุดสิ้นสุดติดกับถนน คลล. ก็นับต่อลง)
- ให้เก็บลูกรังอย่างน้อย 3 ชุดๆ 3 ลูก (ทดสอบลูกรังที่อายุ 28 วัน = 280 ksc. ทรงแบบปกติเมตร) ส่วนแบบคอนกรีต(SLUM) ไม่มากกว่า 7 ซม. ± 2.5 ซม. โดยผู้รับจ้างจะต้องจัดทำเครื่องมือทดสอบ หากค่าความยุบตัว(SLUMP) และแบบหล่อแห่งคอนกรีต ตามที่กำหนดไว้ให้ทำงานให้เพียงพอ
- ให้ผู้รับจ้างดำเนินการทางลาด(ขนาดบ่อ)ทั้งสองข้างทางตลอดสายที่ก่อสร้าง พื้นที่ไม่น้อยกว่า 546 ตารางเมตร
- ให้ผู้รับจ้างชุดหรือพื้นทางเดิม(ลูกรัง) ลึก 0.10 เมตร กว้างไม่น้อยกว่า 7.00 เมตรยาวตลอดสายที่จะทำการก่อสร้าง หรือมีพื้นที่รวมกันไม่น้อยกว่า 3,976 ตารางเมตร
- ปริมาณลูกรังให้ต่ำกว่า ยาวตลอดสาย สองด้านที่ก่อสร้างโดยใช้ปริมาณลูกรังตามที่กำหนดไม่น้อยกว่า 150 ลูกบาศก์เมตร
- รายละเอียดของแบบทามาตราส่วนไม่ชัดเจนให้ชัดเจนให้ดูตัวเลขเป็นเกณฑ์หรือแบบมีการจัดเรียงให้ดูลักษณะของโครงสร้าง

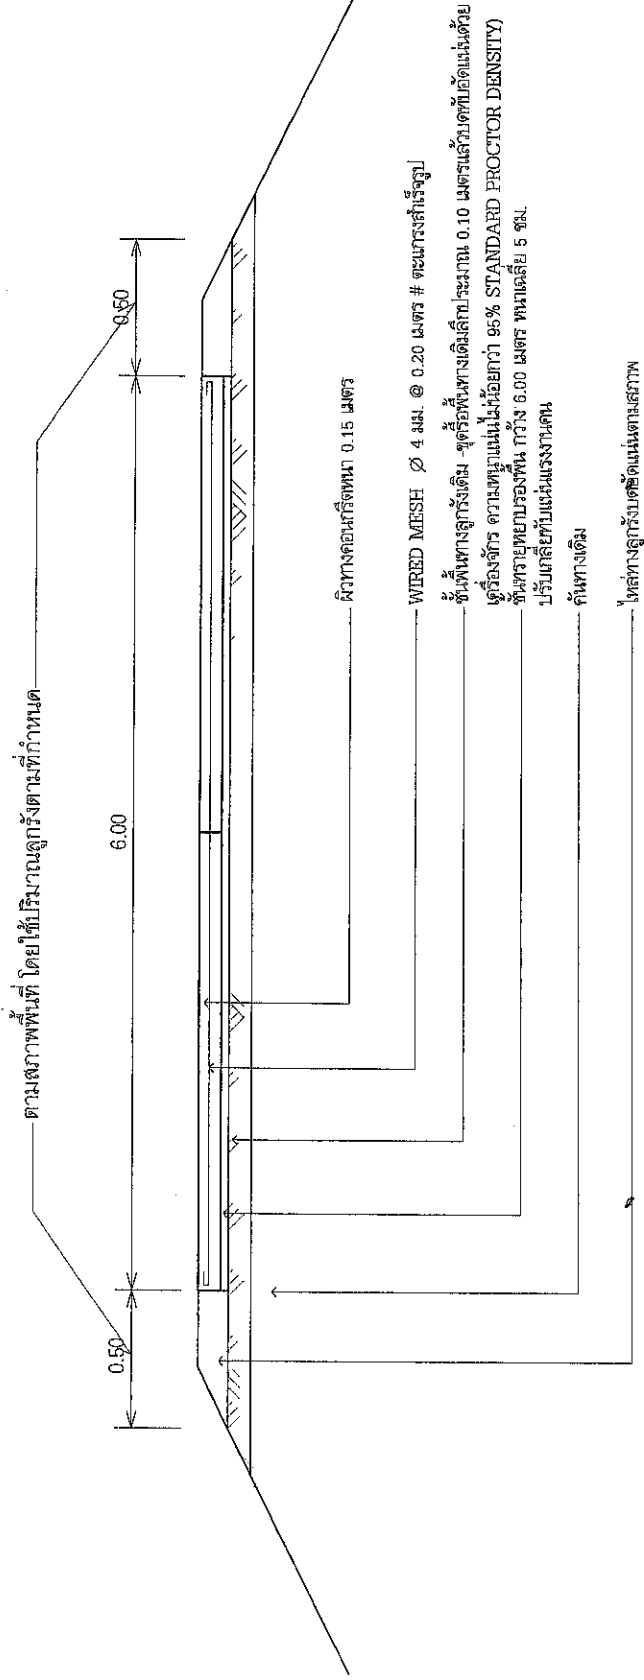

รูปตัดถนนผิวจราจรคอนกรีตเสริมเหล็ก มาตรฐาน 1 : 50

|                                                                    |
|--------------------------------------------------------------------|
| กองช่าง<br>องค์การบริหารส่วนตำบลหัวเขา                             |
| เขียนแบบ / ดำเนินงาน<br>นายโยธิน สร้อยยศย์<br>ผู้ช่วยนายช่างโยธา   |
| เขียนแบบ / ดำเนินงาน<br>นางสาวศุภมาส รอดทอง<br>นายช่างโยธาชำนาญงาน |
| ตรวจ<br>นายสุวิทย์ คุ้มศรี<br>ผู้อำนวยการกองช่าง                   |
| เห็นชอบ<br>จันทนา<br>นางพ ภาณุประทุม<br>ปลัดองค์การบริหารส่วนตำบล  |
| อนุมัติ<br>นายธนู ทองรอด<br>นายกองค์การบริหารส่วนตำบลหัวเขา        |
| แบบโครงการ<br>ก่อสร้างถนนคอนกรีตเสริมเหล็ก<br>หมู่ที่ 4 บ้านวัดไพร |
| แสดง<br>รูปตัดถนน ค.ส.ล. กว้าง 6 เมตร                              |
| จำนวนแผ่นที่ 10/14                                                 |
| วันที่ - มกราคม 2566                                               |
| หมายเหตุ                                                           |


|                                                   |
|---------------------------------------------------|
| กองช่าง                                           |
| องค์การบริหารส่วนตำบลหัวเขา                       |
| เขียนแบบ / สักราว                                 |
| นายโยธิน สร้อยระย้า<br>ผู้ช่วยนายช่างโยธา         |
| เขียนแบบ / สักราว                                 |
| นางสาวกมลรัฐ รอดทอง<br>นายช่างโยธาคำบางขุน        |
| ตรวจสถาปน                                         |
| นายสุวิทย์ ศุภศรีเมือง<br>ผู้อำนวยการกองช่าง      |
| เห็นชอบ<br>จาก                                    |
| นายพ เกษประทุม<br>ปลัดกองการบริหารส่วนตำบล        |
| อนุมัติ                                           |
| นายณัฐ ทองรอด<br>นายกองค์การบริหารส่วนตำบลหัวเขา  |
| แบบโครงการ                                        |
| ก่อสร้างถนนคอนกรีตเสริมเหล็ก<br>หนา 4 นิ้ว 1 เมตร |
| แสดง                                              |
| - 1:1000 หรืออาจลดขนาด 1:500 เมตร                 |
| จำนวนที่ 11/14                                    |
| วันที่ - มกราคม 2566                              |
| หมายเหตุ                                          |

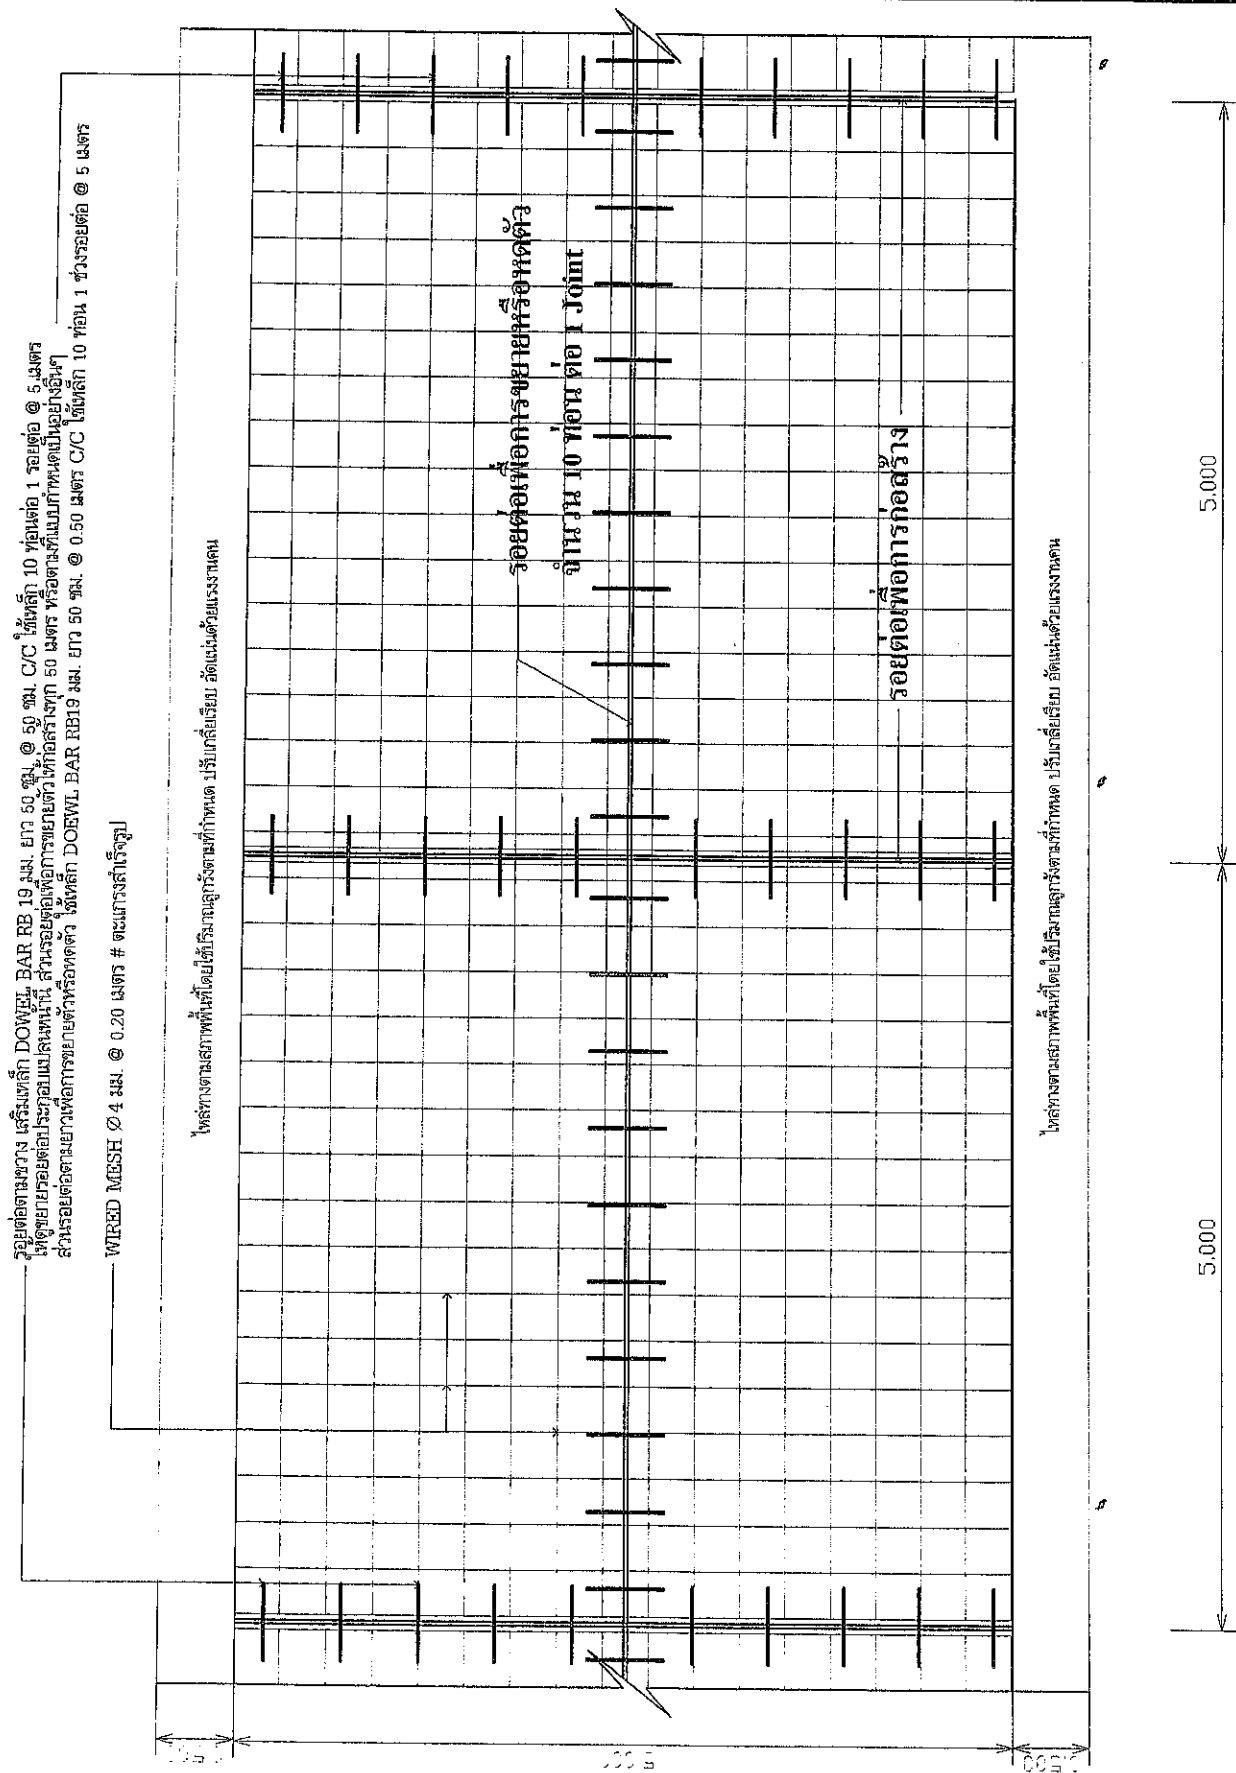


รูปแปลนผิวจราจรคอนกรีต 1:50



|                                                           |
|-----------------------------------------------------------|
| <b>กองช่าง</b>                                            |
| องค์การบริหารส่วนตำบลห้วยเขา                              |
| เขียนแบบ / ลำเนา                                          |
| นายโยธิน ศรีระยา<br>ผู้ชำนาญช่างโยธา                      |
| เขียนแบบ / ลำเนา                                          |
| นางสาวศุภมาส รอดทอง<br>นายช่างโยธาชำนาญงาน                |
| ตรวจ                                                      |
| นายสุรชัย จันทะเรือง<br>ผู้อำนวยการกองช่าง                |
| เห็นชอบ<br>จาก                                            |
| นางพ เกษประทุม<br>ปลัดองค์การบริหารส่วนตำบล               |
| อนุมัติ                                                   |
| นายธน พองรอด<br>นายกองค์การบริหารส่วนตำบลห้วยเขา          |
| แบบโครงการ                                                |
| ก่อสร้างถนนคอนกรีตเสริมเหล็ก<br>หมู่ที่ 4 บ้านวัดไร่      |
| แสดง                                                      |
| - รอยต่อที่ก่อเสริมสร้าง<br>- รอยต่อเพื่อขยายหรือหดตัวได้ |
| จำนวนที่ 13/14                                            |
| วันที่ - มกราคม 2566                                      |
| หมายเหตุ                                                  |

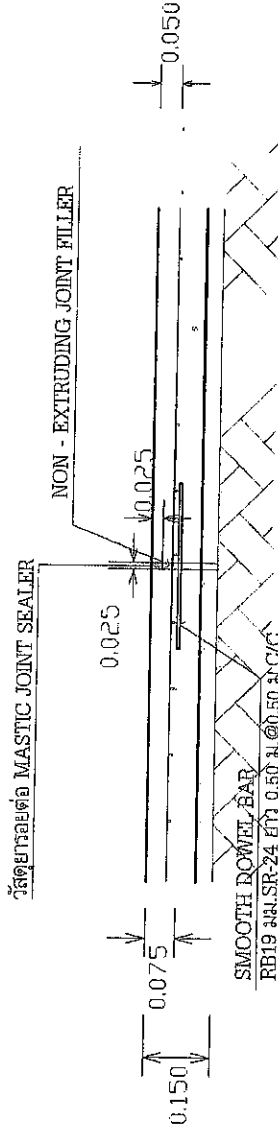

ขยายรอยต่อ EXPANSION JOINT : NOT TO SCALE

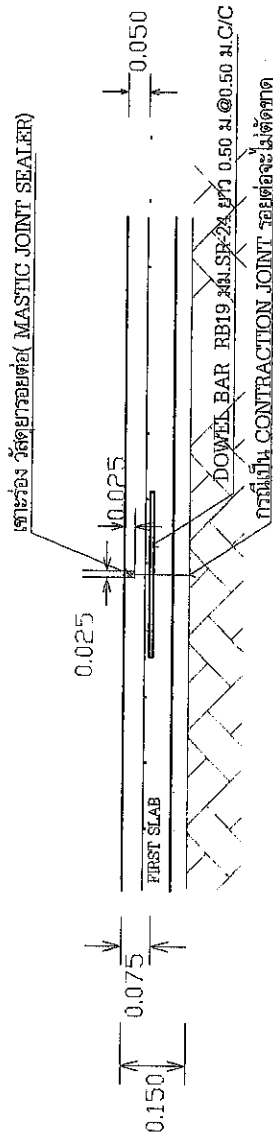

ขยายรอยต่อ CONSTRUCTION JOINT AND CONTRACTION : NOT TO SCALE


## หมายเหตุ รอยต่อคอนกรีต

- ให้ผู้รับจ้างวางแผนโป๊พรอยต่อถนนเดิมพร้อมหมุดตาง(ไม่ต้องเจาะเสริมเหล็ก)ตามแบบรอยต่อเพื่อขยายตัวโดยให้เสริมเหล็กที่ยึดติดของถนนหรือจุดสิ้นสุดโครงการให้เป็นไปตามรอยต่อเพื่อการก่อสร้างครั้งต่อไป ซึ่งหากเป็นจุดสิ้นสุดถนนไม่ต้องใส่เหล็ก

# หมายเหตุ



- ให้ผู้รับจ้างทำการตัดดินให้ระดับที่จะทำการก่อสร้าง โดยให้ยี่ตรงระดับเสมอแล้วเสร็จกับระดับของถนน ค.ส.ล.เดิมเป็นเกณฑ์ โดยเพิ่มความลึกไม่น้อยกว่า 0.20 เมตร (ความหนาชั้นทรายของพื้น 0.05 เมตร + ความหนาชั้นผิวทาง ค.ส.ล. 0.15 เมตร)
- มาตราฐานการก่อสร้าง เหมือนกับ การก่อสร้างถนนหลัก โดยให้มีระยะ ขอบเขตตามแบบกำหนด ห้ามวัดระยะจากแบบโดยเด็ดขาด หากระยะ หรือรูปแบบใดไม่ชัดเจนให้สอบถามจากผู้ควบคุมงาน
- ระยะตามที่แบบกำหนด อาจมีการเปลี่ยนแปลงได้ ตามสภาพงานจริงและปัญหาอุปสรรคที่เกิดขึ้นระหว่างทำการก่อสร้างหากมีความจำเป็น ผู้ควบคุมงานและคณะกรรมการตรวจสอบจะรับฟังข้อเท็จจริงจากผู้กำหนดใหม่ และไม่ถือเป็นการแก้ไขเปลี่ยนแปลงรูปแบบหรือสัญญาจ้างแต่ประการใด โดยจะยึดถือเงื่อนไขตามรูปแบบการจ้างเดิม และปริมาณพื้นที่ก่อสร้างโดยรวมเป็นเกณฑ์

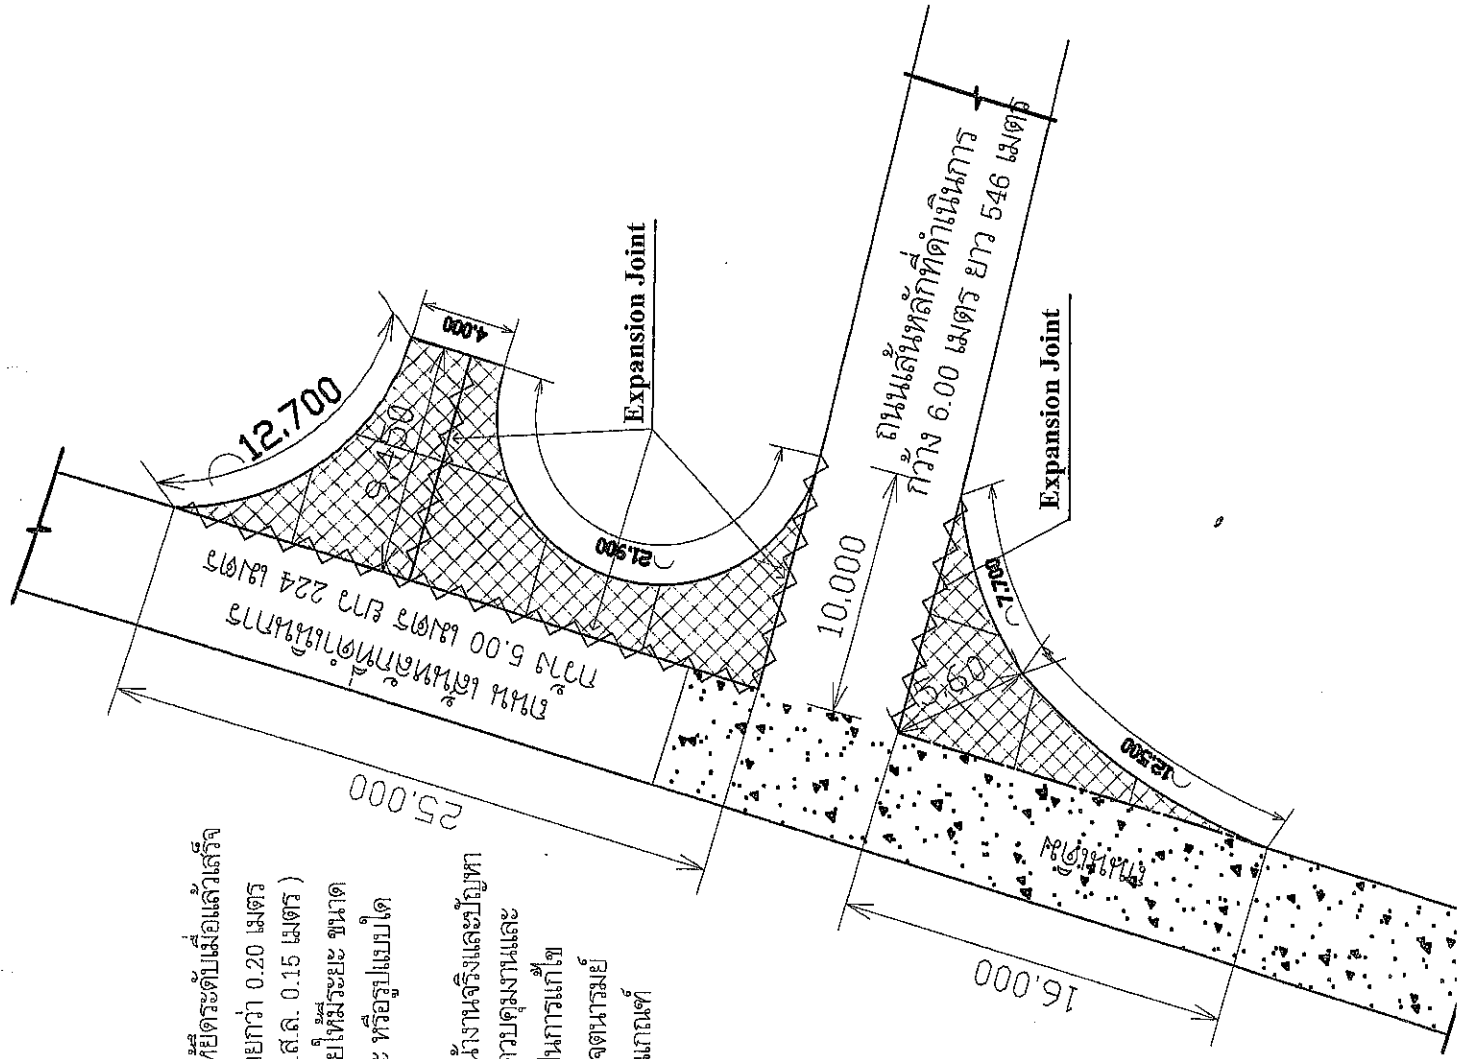

|                             |                                                                |
|-----------------------------|----------------------------------------------------------------|
| กองช่าง                     |                                                                |
| องค์การบริหารส่วนตำบลห้วยผา |                                                                |
| สำรวจ/เขียนแบบ              | นายโยธิน ศรีระยา<br>ผู้ช่วยนายก อบ.ต.ห้วยผา                    |
| สำรวจ/เขียนแบบ              | นางสาวสุวิมล รอดทอง<br>นายก อบ.ต.ห้วยผา                        |
| ตรวจ/อนุมัติ                | นายสุวิมล รอดทอง<br>นายก อบ.ต.ห้วยผา                           |
| เห็นชอบ                     | นายสุวิมล รอดทอง<br>นายก อบ.ต.ห้วยผา                           |
| อนุมัติ                     | นายสุวิมล รอดทอง<br>นายก อบ.ต.ห้วยผา                           |
| นายสุวิมล รอดทอง            | นายก อบ.ต.ห้วยผา                                               |
| แบบ/โครงการ                 | ก่อสร้างถนนคอนกรีตเสริมเหล็ก<br>พื้นที่ 4 ไร่ 1 งาน 10 ตารางวา |
| แสดง                        | - แปลงทางเชื่อม ค.ส.ล.                                         |
| จำนวนแผ่นที่                | 14/14                                                          |
| วันที่                      | มกราคม 2566                                                    |